

GENERAL NOTES:

DO NOT SCALE DRAWINGS. FIGURE DIMENSIONS TAKE PRECEDENCE OVERALL.

THESE DRAWINGS ARE TO BE READ IN CONJUNCTION WITH ENGINEERS COMPUTATIONS AND DRAWINGS.

THE BUILDER AND SUBCONTRACTOR SHALL CHECK AND VERIFY ALL DIMENSIONS, SETBACKS, LEVELS AND SPECIFICATIONS AND ALL OTHER RELEVANT DOCUMENTATION PRIOR TO THE COMMENCEMENT OF ANY WORKS. REPORT ALL DISCREPANCIES TO THIS OFFICE FOR CLARIFICATION.

INSTALLATION OF ALL SERVICES SHALL COMPLY WITH THE RESPECTIVE SUPPLY AUTHORITY REQUIREMENTS.

ALL WORK TO COMPLY WITH THE BUILDING CODE OF AUSTRALIA, OTHER RELEVANT BYLAWS & AUTHORITIES.

ALL GLASS TO COMPLY WITH AS 1288-2006
ALL MASONRY TO COMPLY WITH AS 3700-2011
ALL TIMBER TO COMPLY WITH AS 1684-2006
ALL SMOKE DETECTORS TO COMPLY WITH AS3786-1993
WATERPROOFING TO COMPLY WITH AS3740-2010

ALL HANDRAILS AND BALUSTRADES TO COMPLY WITH NCC VOL.2 PART 3.8.3.3.

UNLESS NOTED, EXCAVATIONS TO BE BATTERED AT 45° MAX. FOR SAND/SILT/FILL SITES ALL BATTERS TO BE KEPT WITHIN PROPERTY BOUNDARIES.

THE BUILDER AND SUBCONTRACTOR SHALL ENSURE THAT ALL STORMWATER DRAINS, SEWER PIPES AND THE LIKE ARE FOOTING AND/OR SLAB EDGE BEAMS SO AS TO PREVENT MOISTURE PENETRATION, DAMPNESS, WEAKENING AND UNDERMINING OF ANY BUILDING AND ITS FOOTING SYSTEM.

LOCATION OF ALL SERVICES IS INDICITIVE ONLY.

DOWNPIPES TO SERVE <12M OF GUTTER. INSTALL DOWNPIPE WITHIN 1200mm OF VALLEY OR PROVIDE OVERFLOWS TO GUTTER.

INSULATION TO BE AS PER SPECIFICATION & TO BE READ IN CONJUNCTION WITH ENERGY REPORT.

DOORS TO WC TO HAVE LIFT OF HINGES, UNLESS 1200mm CLEAR BETWEEN PAN & DOORWAY.

STEP SIZES(EXC. SPIRAL STAIRS) TO BE: RISERS (R) 190mm MAX. & 115mm MIN. GOING (G) 355mm MAX. & 240mm MIN. 2R + 1G = 700mm MAX. & 550mm MIN. WHERE NO STEP PROVIDED, SITE MUST BE GRADED TO ENSURE MAXIMUM STEP DOWN OF 190mm FROM EXTERNAL DOOR TO FSL.

DRAINAGE REQUIREMENTS:

SURFACE DRAINAGE OF THE SITE SHALL BE CONTROLLED FROM THE START OF SITE PREPARATION AND CONSTRUCTION. THE DRAINAGE SYSTEM SHALL BE COMPLETED BY THE FINISH OF CONSTRUCTION OF THE BUILDING.

SUBSURFACE DRAINS TO REMOVE GROUNDWATER SHALL BE DESIGNED IN ACCORDANCE WITH ENGINEERING PRINCIPLES.

PLUMBING REQUIREMENTS:

DRAINS ATTACHED TO/OR EMERGING FROM UNDERNEATH THE BUILDING SHALL INCORPORATE FLEXIBLE JOINTS IMMEDIATELY OUTSIDE THE FOOTING AND COMMENCING WITHIN 1.0M OF THE BUILDING PERIMETER TO ACCOMODATE A TOTAL RANGE OF DIFFERENTIAL MOVEMENT IN ANY DIRECTION EQUAL TO THE ESTIMATED CHARACTERISTIC SURFACE MOVEMENT OF THE SITE. THIS REQUIREMENT APPLIES TO ALL STORMWATER AND SANITARY PLUMBING DRAINS AND DISCHARGE PIPES.

THE BUILDER AND SUBCONTRACTOR SHALL ENSURE THAT ALL STORMWATER DRAINS, SEWER PIPES AND THE LIKE ARE LOCATED AT A SUFFICIENT DISTANCE FROM ANY BUILDINGS FOOTING AND/OR SLAB EDGE BEAMS SO AS TO PREVENT MOISTURE PENETRATIO, DAMPNESS, WEAKENING AND UNDERMINING OF ANY BUILDING AND ITS FOOTING SYSTEM.

LOCATION OF STORMWATER SYSTEM/S ARE INDICITIVE ONLY

DOWNPIPES TO SERVE <12m OF GUTTER. INSTALL A DOWNPIPE WITHIN 1200MM OF VALLEY OR PROVIDE OVERFLOWS TO GUTTER.

SITE PREPARATION REQUIREMENTS:

UNLESS NOTED OTHERWISE, EXCAVATIONS TO BE BATTERED AT MAX. 45° FOR SAND/SILT/FILL SITES.ALL BATTERS TO BE KEPT WITHIN PROPERTY BOUNDARIES.

ALL CUT & FILL BATTERS MUST BE STABILISED FOLLOWING CONSTRUCTION. THE GROUND LEVEL IMMEDIATELY ADJACENT TO THE BUILDING SHALL BE GRADED TO A UNIFORM FALL OF MIN. 50mm AWAY FROM THE BUILDING OVER THE FIRST METRE.

PROVIDE AGRICULTURAL DRAIN TO THE BASE OF THE SITE CUT CONNECTED TO THE STORMWATER SYSTEM VIA SILT PIT WHERE SITE CUT IS GREATER THAN 300MM.

PROVIDE CUT TOE OR SPOON DRAIN @ MIN. FALL TO BASE OF SITE CUT CONNECTED TO STORMWATER SYSTEM VIA SILT PIT WHERE SITE CUT IS LESSER THAN 300MM.



DRAWING TITLE:

Title Page

DRAWING NO:
01

PROJECT NO:
TMD2221

PROJECT ADDRESS:

32 RICHARDSON STREET
CHELMER QLD 4068

ISSUE DATE:

7TH DECEMBER 2022

REVISION:

Rev M

CLIENT:

L. RICHARDSON

AUTHOR:

TM

DISCLAIMER:

THE PLAN & DESIGN OF THIS HOUSE IS OWNED BY
MARSHALL DESIGN PTY LTD AND UNDER THE
COPYRIGHT ACT OF 1964 CANNOT BE REPRODUCED IN
ANY SHAPE OR FORM WITHOUT PRIOR WRITTEN
CONSENT. ANY DOING SO WILL RESULT IN LIABILITY
UNDER THE ACT.



SITE SETOUT AND DIMENSIONS:

SITE SETOUT AND DIMENSIONS TO BE
CONFIRMED WITH FINAL SURVEY PLANS
BEFORE ANY WORK IS TO COMMENCE.

TERMITE TREATMENT:

PROVIDE TERMITE PROTECTION IN
ACCORDANCE WITH AS3660.1

SITE PREPARATION REQUIREMENTS:

UNLESS NOTED OTHERWISE, EXCAVATIONS
TO BE BATTERED AT MAX. 45° FOR
SAND/SILT/FILL SITES.ALL BATTERS TO BE
KEPT WITHIN PROPERTY BOUNDARIES.

ALL CUT & FILL BATTERS MUST BE
STABILISED FOLLOWING CONSTRUCTION.
THE GROUND LEVEL IMMEDIATELY
ADJACENT TO THE BUILDING SHALL BE
GRADED TO A UNIFORM FALL OF MIN. 50mm
AWAY FROM THE BUILDING OVER THE FIRST
METRE.

PROVIDE AGRICULTURAL DRAIN TO THE
BASE OF THE SITE CUT CONNECTED TO THE
STORMWATER SYSTEM VIA SILT PIT WHERE
SITE CUT IS GREATER THAN 300MM.

PROVIDE CUT TOE OR SPOON DRAIN @ MIN.
FALL TO BASE OF SITE CUT CONNECTED TO
STORMWATER SYSTEM VIA SILT PIT WHERE
SITE CUT IS LESSER THAN 300MM.

PROPERTY DESCRIPTION:

LOT 64 ON RP29383

COUNTY OF

LOCALITY: CHELMER

LOCAL GOVERNMENT: BRISBANE CITY
COUNCIL


SITE AREA: 435m²

SITE ANALYSIS:

BUILDING AREA: 185.00m²

SITE AREA: 435m²

SITE COVERAGE: 42.53%

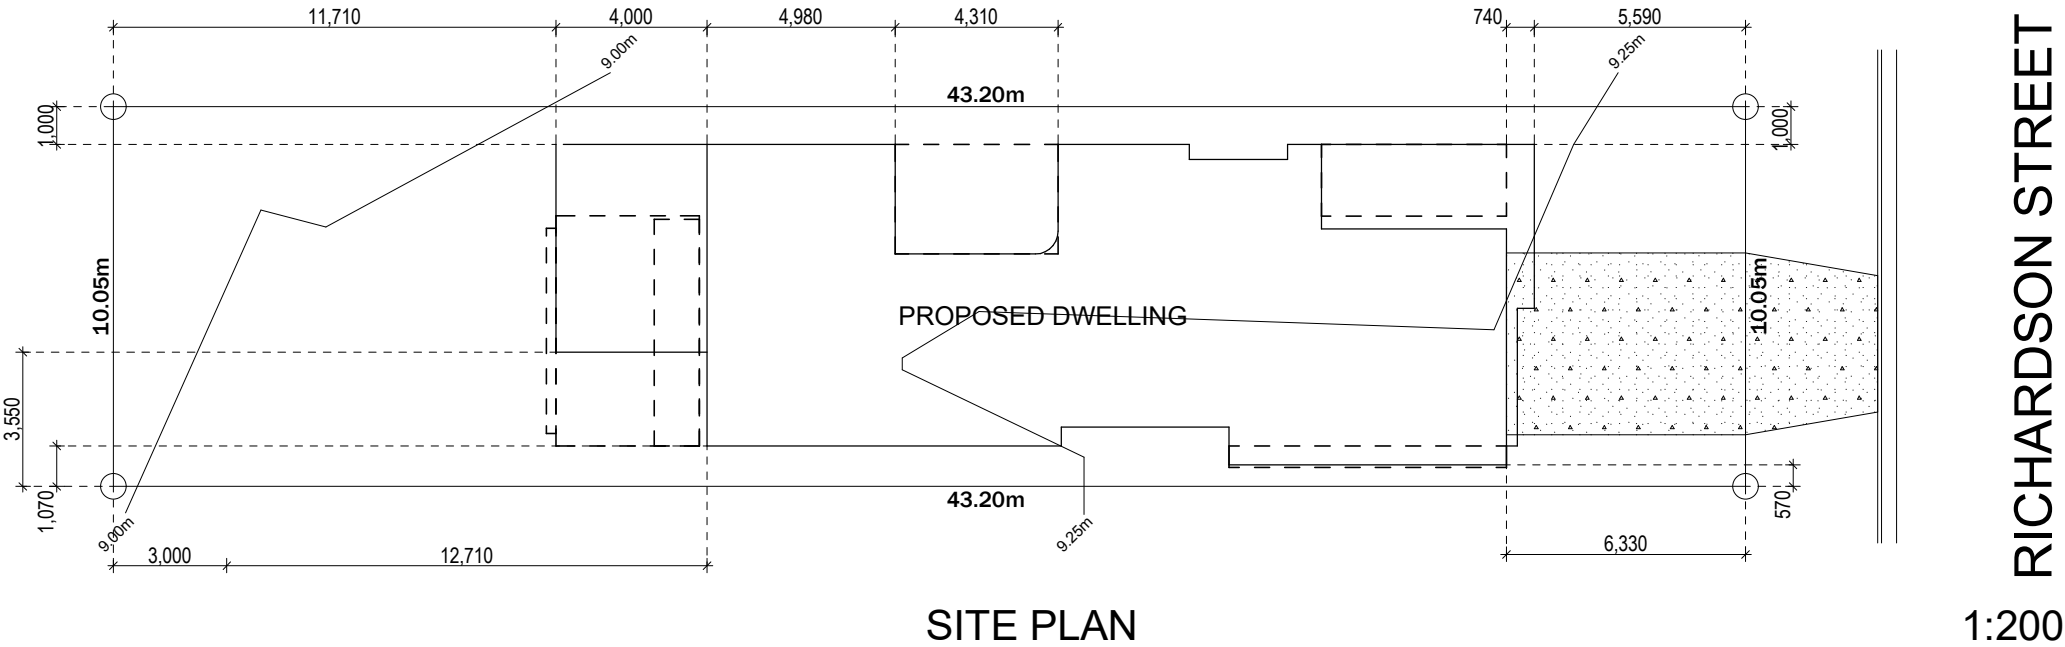

DRAWING TITLE:

Site Plan

DRAWING NO:

02

PROJECT NO:

TMD2221

PROJECT ADDRESS:

32 RICHARDSON STREET
CHELMER QLD 4068

ISSUE DATE:

7TH DECEMBER 2022

REVISION:

Rev M

CLIENT:

L. RICHARDSON


AUTHOR:

TM

DISCLAIMER:

THE PLAN & DESIGN OF THIS HOUSE IS OWNED BY
TMARSHALL DESIGN PTY LTD AND UNDER THE
COPYRIGHT ACT OF 1984 CANNOT BE REPRODUCED IN
ANY SHAPE OR FORM WITHOUT PRIOR WRITTEN
CONSENT. ANY DOING SO WILL RESULT IN LIABILITY
UNDER THE ACT.



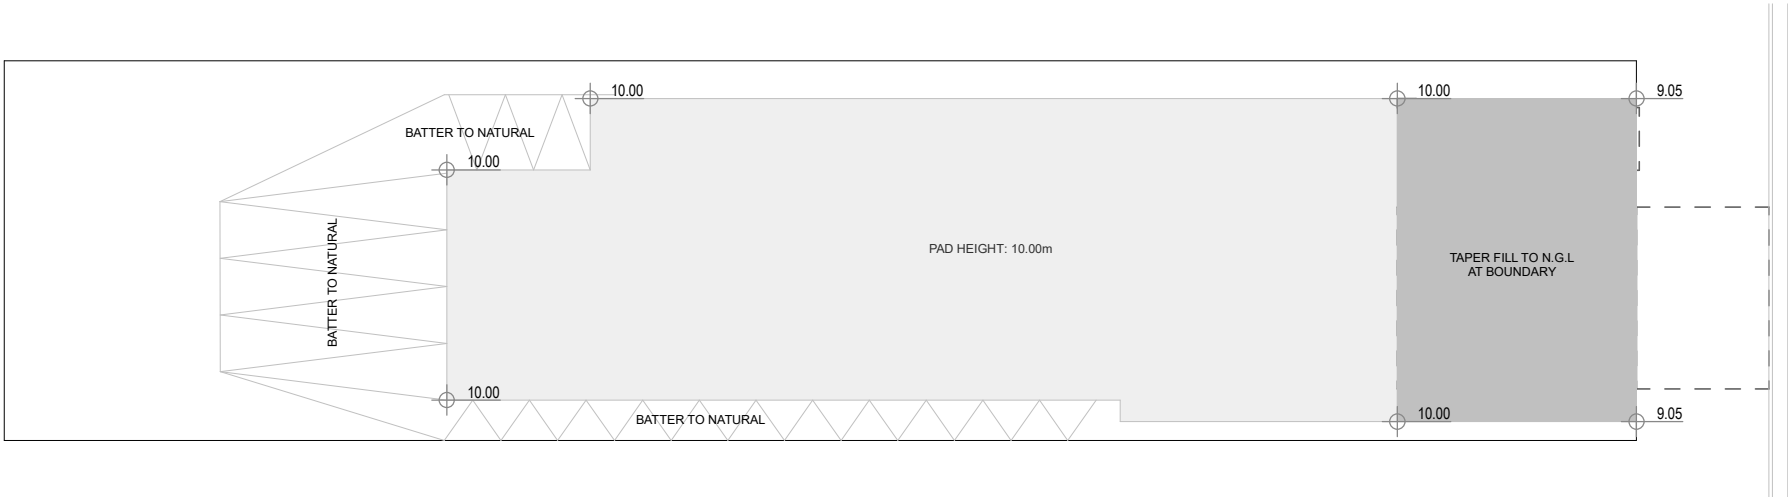

EXTERNAL WORKS

1:200



DRAWING TITLE:

External Works

DRAWING NO:

03

PROJECT NO:

TMD2221

PROJECT ADDRESS:

32 RICHARDSON STREET
CHELMER QLD 4068

ISSUE DATE:

7TH DECEMBER 2022

REVISION:

Rev M

CLIENT:

L. RICHARDSON


AUTHOR:

TM

DISCLAIMER:


THE PLAN & DESIGN OF THIS HOUSE IS OWNED BY
TMARSHALL DESIGN PTY LTD AND UNDER THE
COPYRIGHT ACT OF 1984 CANNOT BE REPRODUCED IN
ANY SHAPE OR FORM WITHOUT PRIOR WRITTEN
CONSENT. ANY DOING SO WILL RESULT IN LIABILITY
UNDER THE ACT.



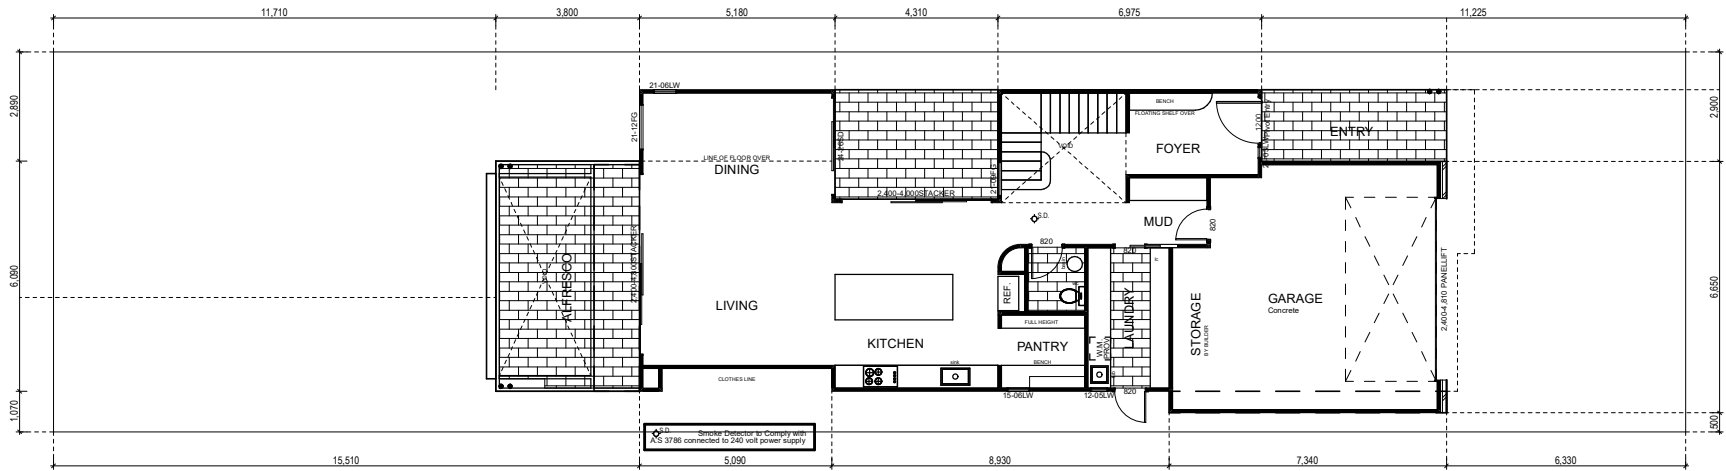

GROUND FLOOR - SETBACK

1:200

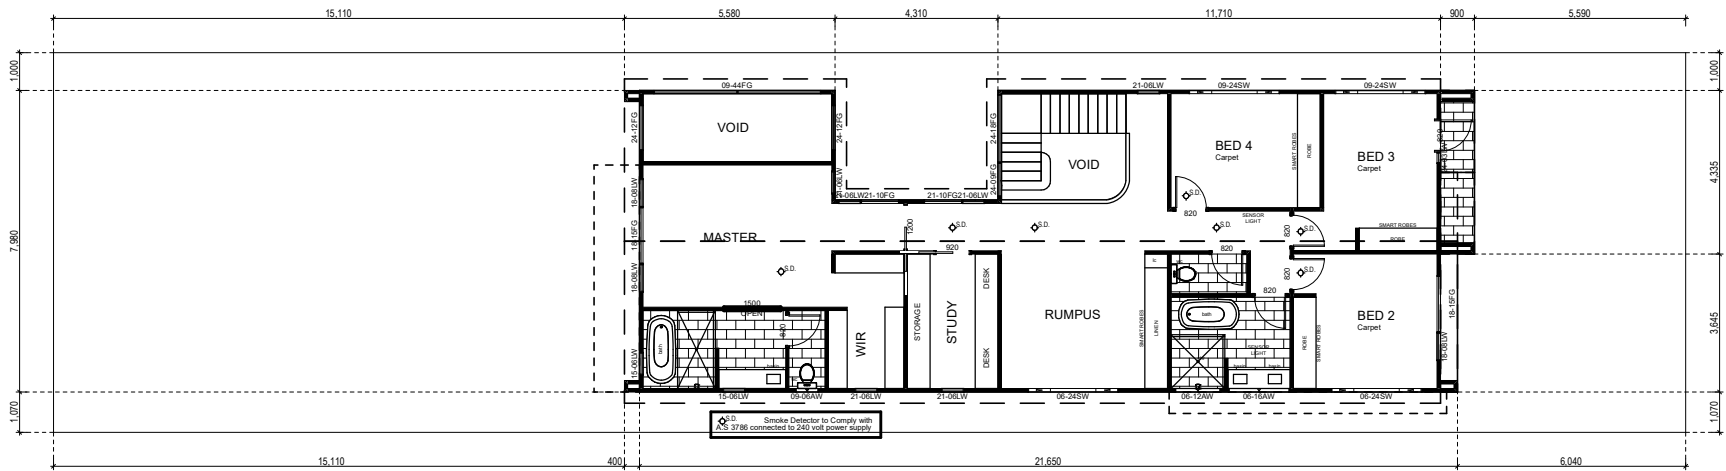

FIRST FLOOR - SETBACK

1:200

DRAWING TITLE:

Setback Plans

DRAWING NO:	PROJECT NO:
04	TMD2221

PROJECT ADDRESS:

**32 RICHARDSON STREET
CHELMER QLD 4068**

ISSUE DATE:

7TH DECEMBER 2022

REVISION:

Rev M

CLIENT:


L. RICHARDSON

AUTHOR:

TM

DISCLAIMER:

THE PLAN & DESIGN OF THIS HOUSE IS OWNED BY
TMD DESIGN PTY LTD AND UNDER THE
COPYRIGHT ACT OF 1984 CANNOT BE REPRODUCED IN
ANY SHAPE OR FORM WITHOUT PRIOR WRITTEN
CONSENT. ANY DOING SO WILL RESULT IN LIABILITY
UNDER THE ACT.

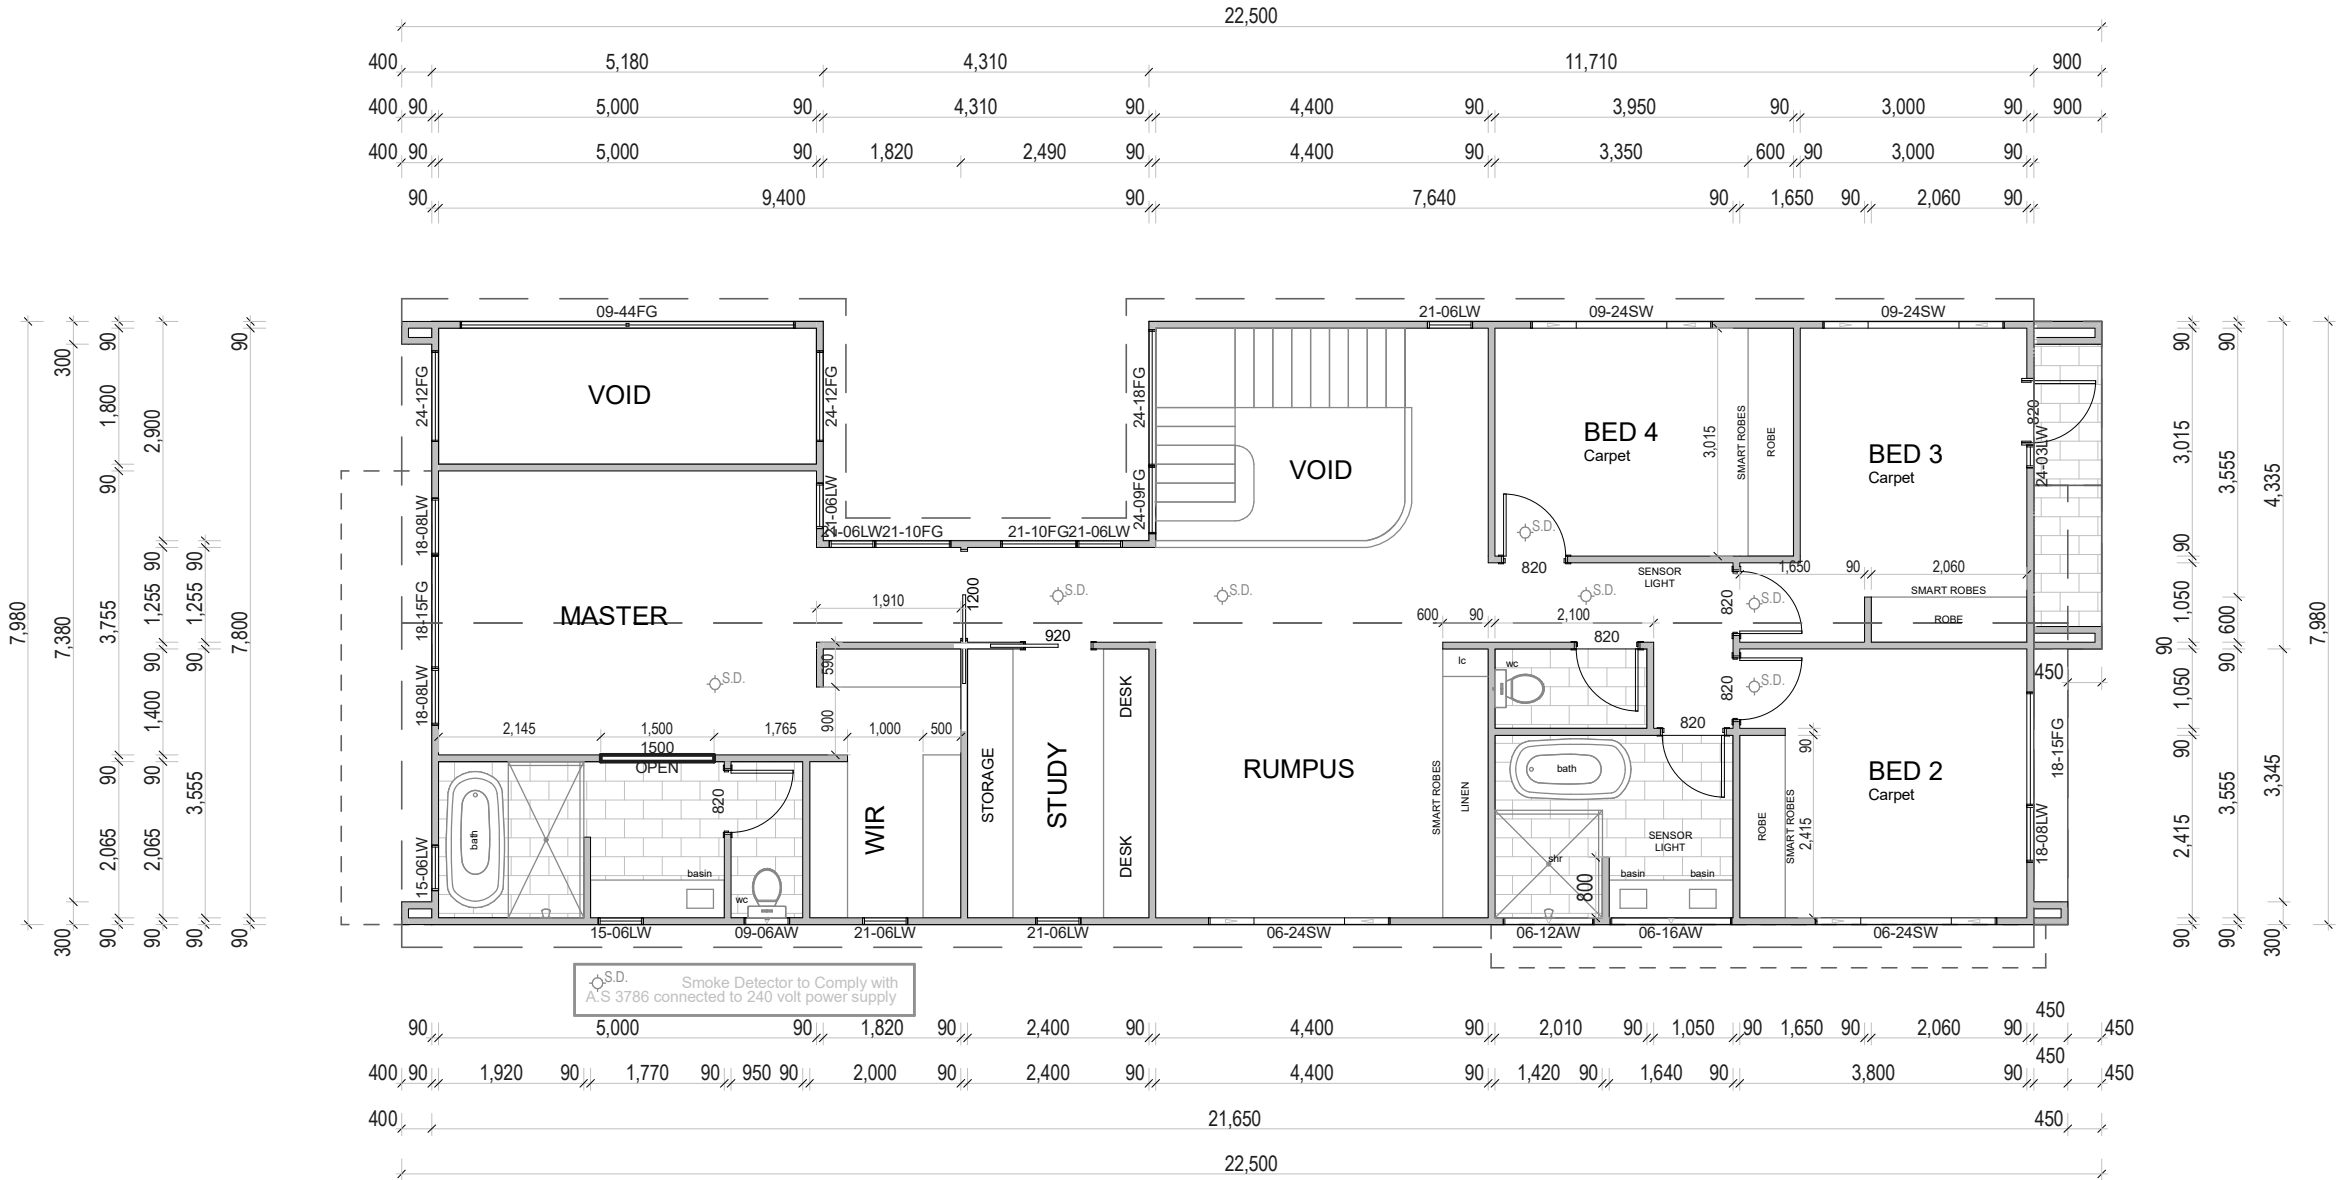

FIRST FLOOR

1:100



DRAWING TITLE:

First Floor

DRAWING NO:
06

PROJECT NO:
TMD2221

PROJECT ADDRESS:

32 RICHARDSON STREET
CHELMER QLD 4068

ISSUE DATE:

7TH DECEMBER 2022

REVISION:

Rev M

CLIENT:

L. RICHARDSON


AUTHOR:

TM

DISCLAIMER:


THE PLAN & DESIGN OF THIS HOUSE IS OWNED BY
T MARSHALL DESIGN PTY LTD AND UNDER THE
COPYRIGHT ACT OF 1984 CANNOT BE REPRODUCED IN
ANY SHAPE OR FORM WITHOUT PRIOR WRITTEN
CONSENT. ANY DOING SO WILL RESULT IN LIABILITY
UNDER THE ACT.



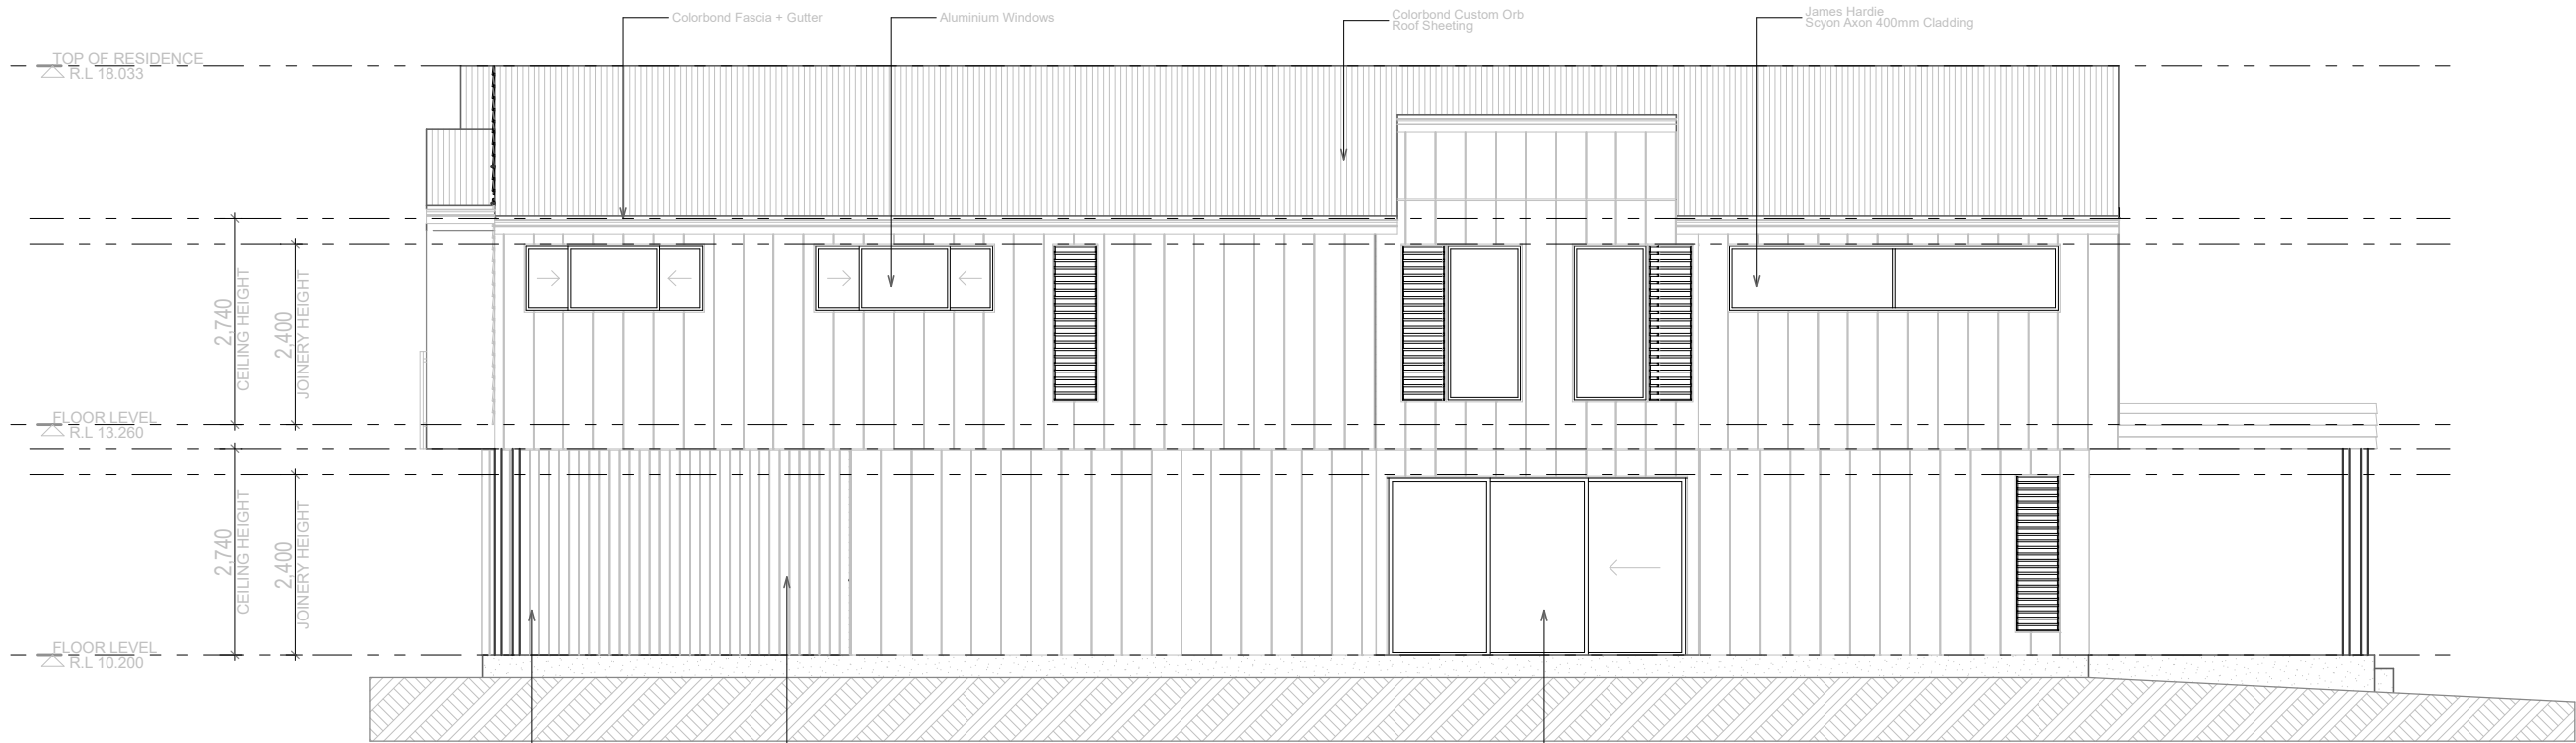

NORTH ELEVATION

1:100

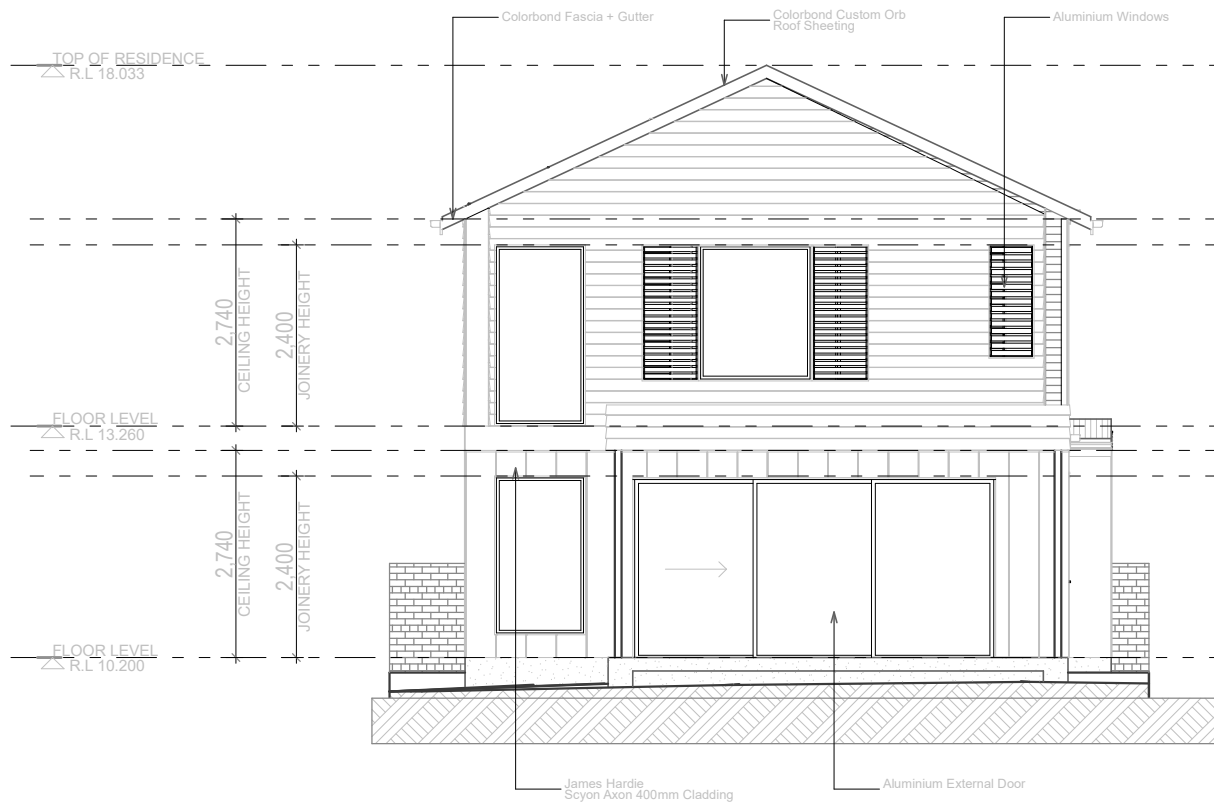


WEST ELEVATION

1:100




DRAWING TITLE: Elevations 1	
DRAWING NO: 07	PROJECT NO: TMD2221
PROJECT ADDRESS: 32 RICHARDSON STREET CHELMER QLD 4068	
ISSUE DATE: 7TH DECEMBER 2022	
REVISION: Rev M	
CLIENT: L. RICHARDSON	
AUTHOR: TM	
DISCLAIMER: THE PLAN & DESIGN OF THIS HOUSE IS OWNED BY MARSHALL DESIGN PTY LTD AND UNDER THE COPYRIGHT ACT OF 1984 CANNOT BE REPRODUCED IN ANY SHAPE OR FORM WITHOUT PRIOR WRITTEN CONSENT. ANY DOING SO WILL RESULT IN LIABILITY UNDER THE ACT.	



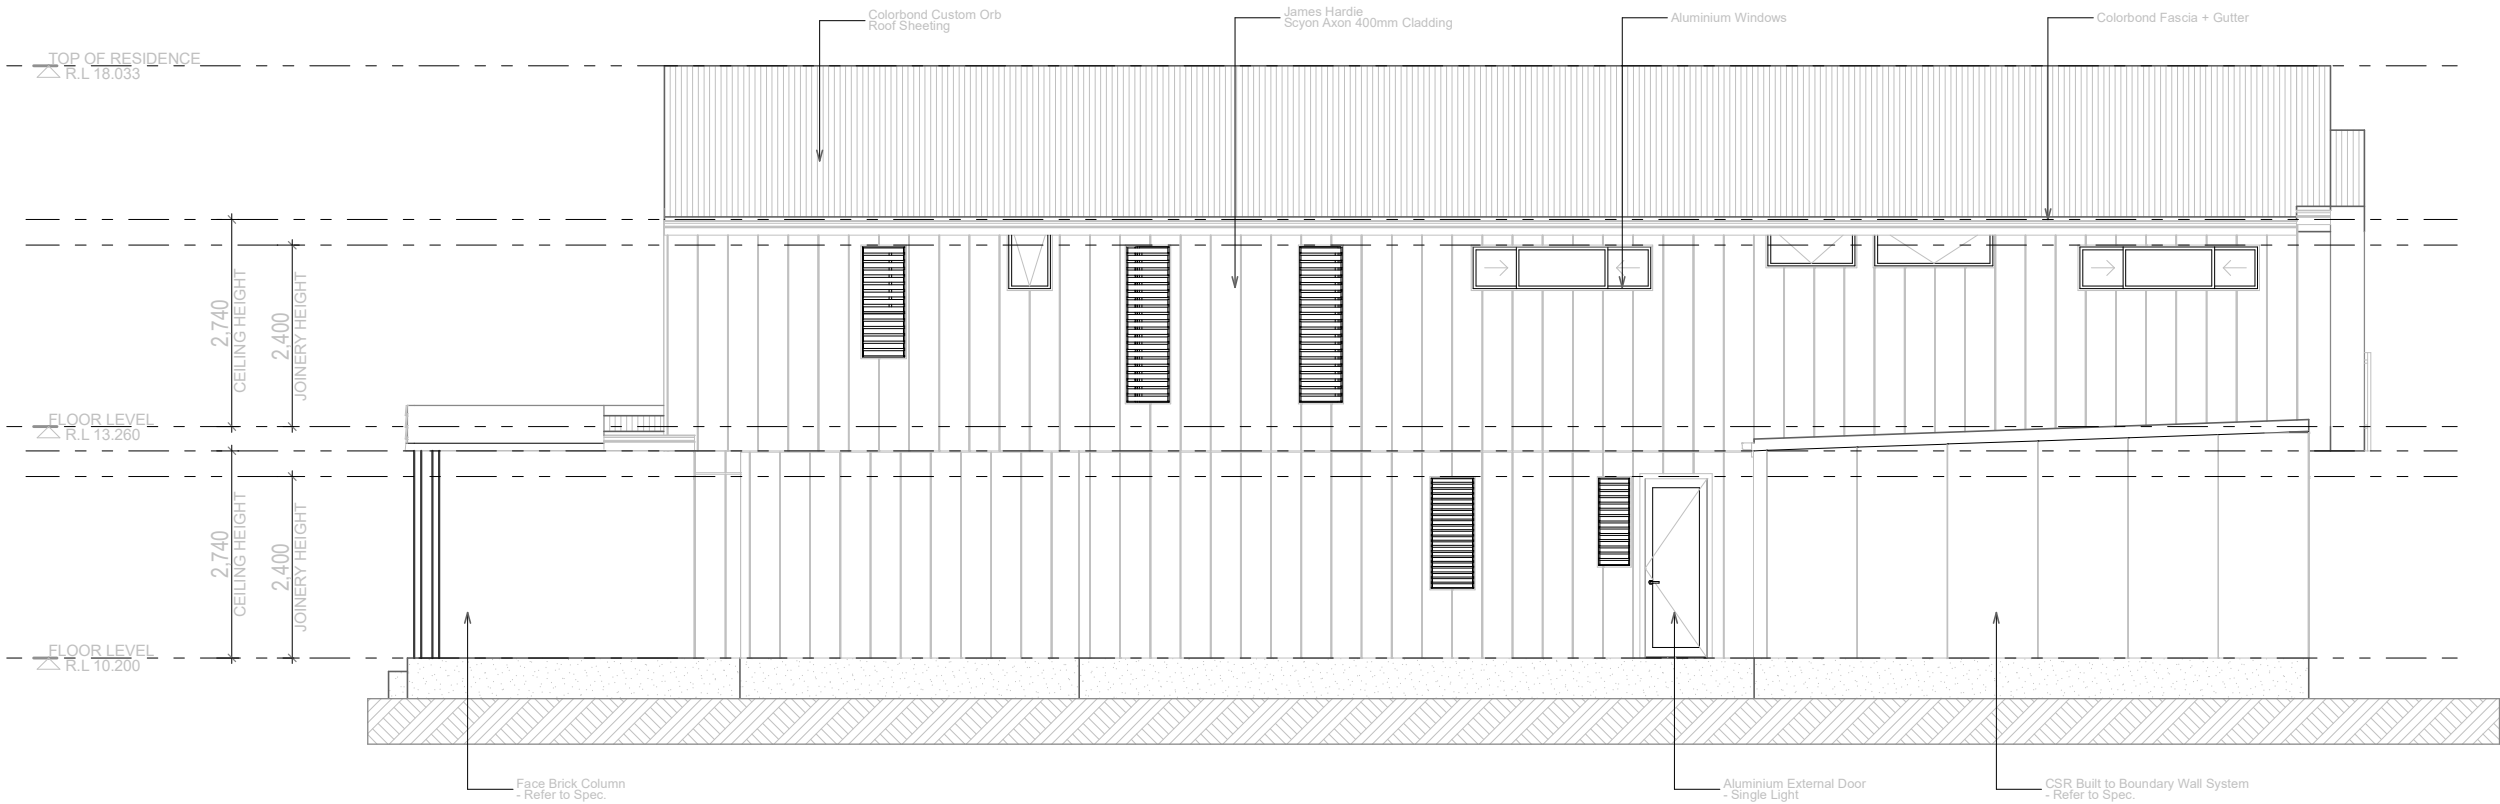

SOUTH ELEVATION

1:100

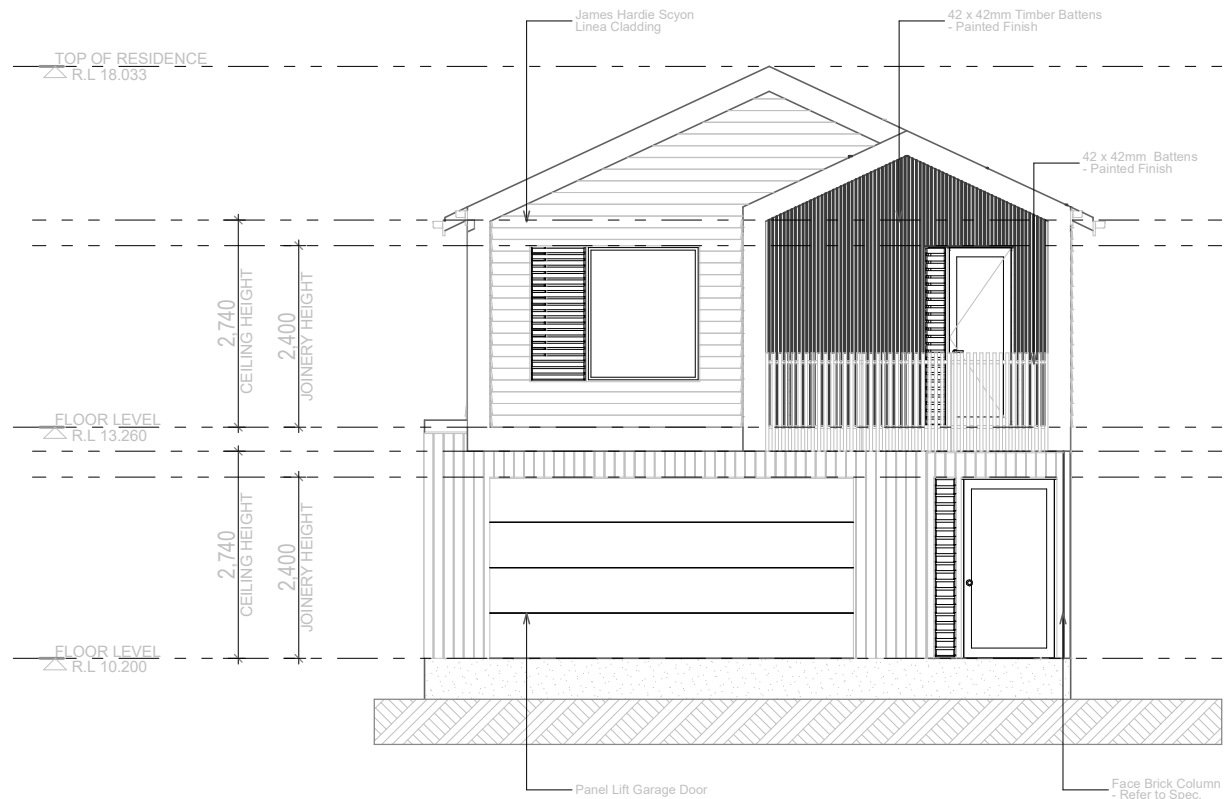

EAST ELEVATION

1:100



DRAWING TITLE:

Elevations 2

DRAWING NO:

08

PROJECT NO:

TMD2221

PROJECT ADDRESS:

32 RICHARDSON STREET
CHELMER QLD 4068

ISSUE DATE:

7TH DECEMBER 2022

REVISION:

Rev M

CLIENT:

L. RICHARDSON


AUTHOR:

TM

DISCLAIMER:


THE PLAN & DESIGN OF THIS HOUSE IS OWNED BY
MARSHALL DESIGN PTY LTD AND UNDER THE
COPYRIGHT ACT OF 1964 CANNOT BE REPRODUCED IN
ANY SHAPE OR FORM WITHOUT PRIOR WRITTEN
CONSENT. ANY DOING SO WILL RESULT IN LIABILITY
UNDER THE ACT.



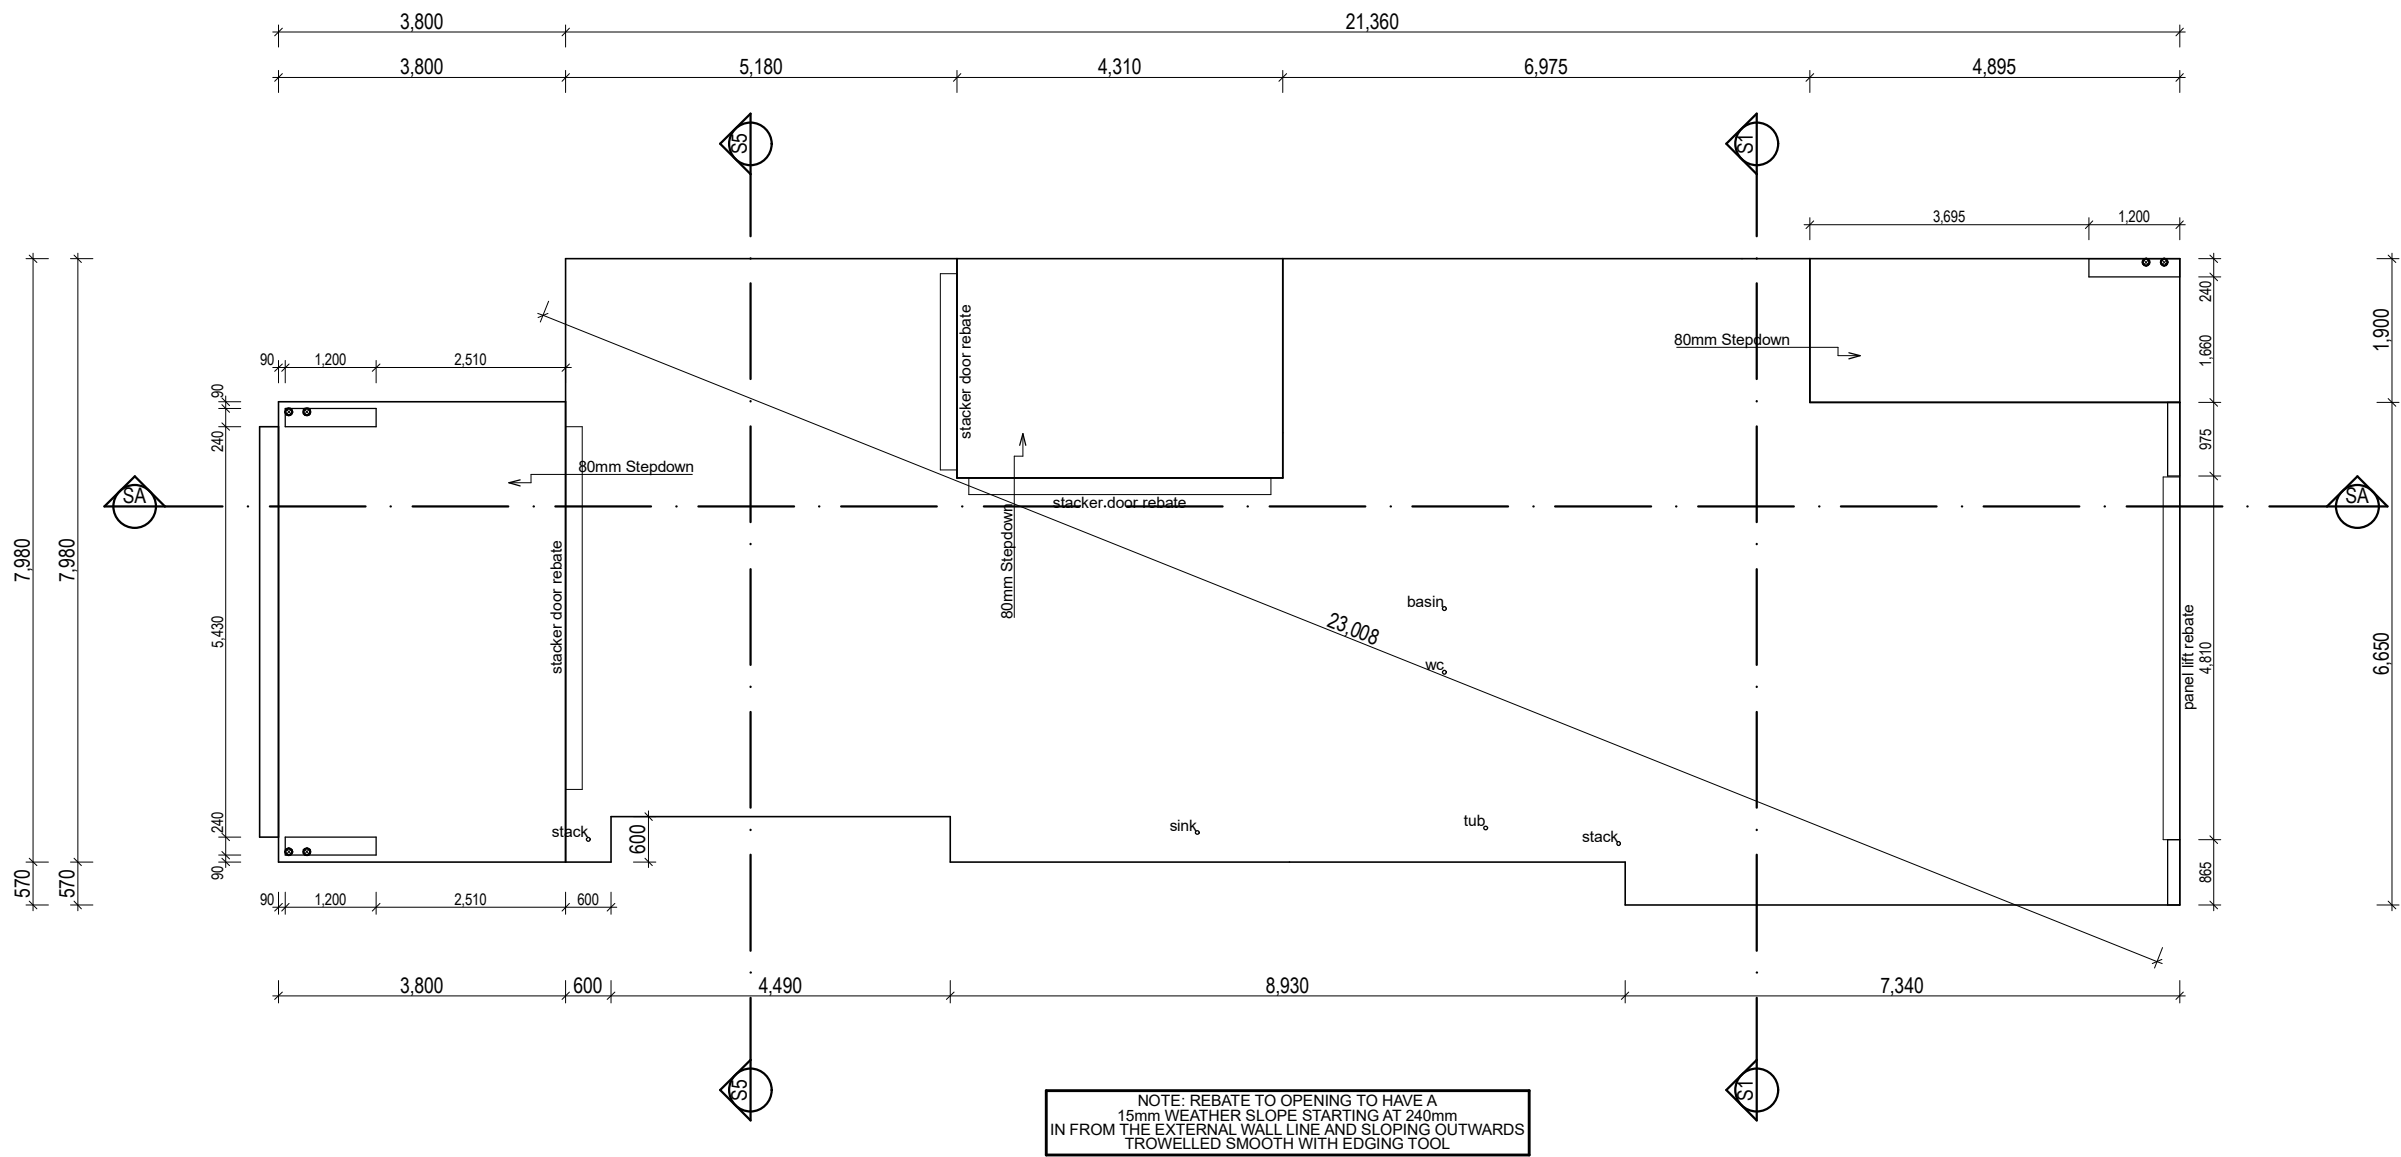

SLAB PLAN

1:100

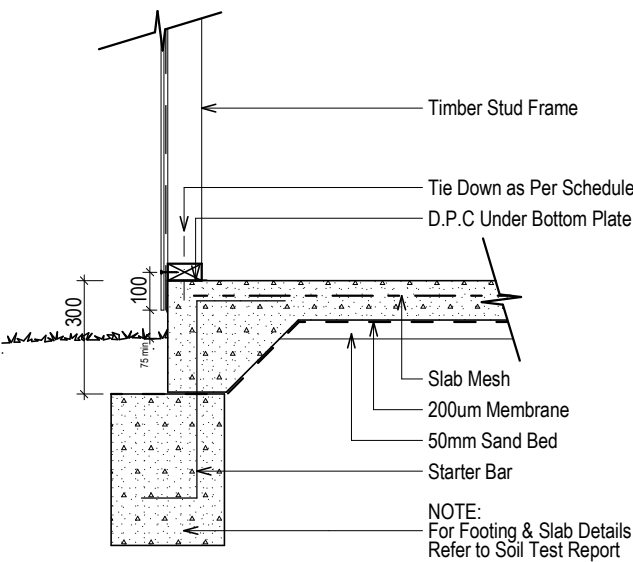

TIMBER FRAME W/ FC CLADDING OR WEATHERBOARDS -
SLAB ON GROUND

DRAWING TITLE:

Slab Plan

DRAWING NO:	PROJECT NO:
09	TMD2221

PROJECT ADDRESS:

**32 RICHARDSON STREET
CHELMER QLD 4068**

ISSUE DATE:

7TH DECEMBER 2022

REVISION:

Rev M

CLIENT:


L. RICHARDSON

AUTHOR:

TM

DISCLAIMER:

THE PLAN & DESIGN OF THIS HOUSE IS OWNED BY MARSHALL DESIGN PTY LTD AND UNDER THE COPYRIGHT ACT OF 1984 CANNOT BE REPRODUCED IN ANY SHAPE OR FORM WITHOUT PRIOR WRITTEN CONSENT. ANY DOING SO WILL RESULT IN LIABILITY UNDER THE ACT.

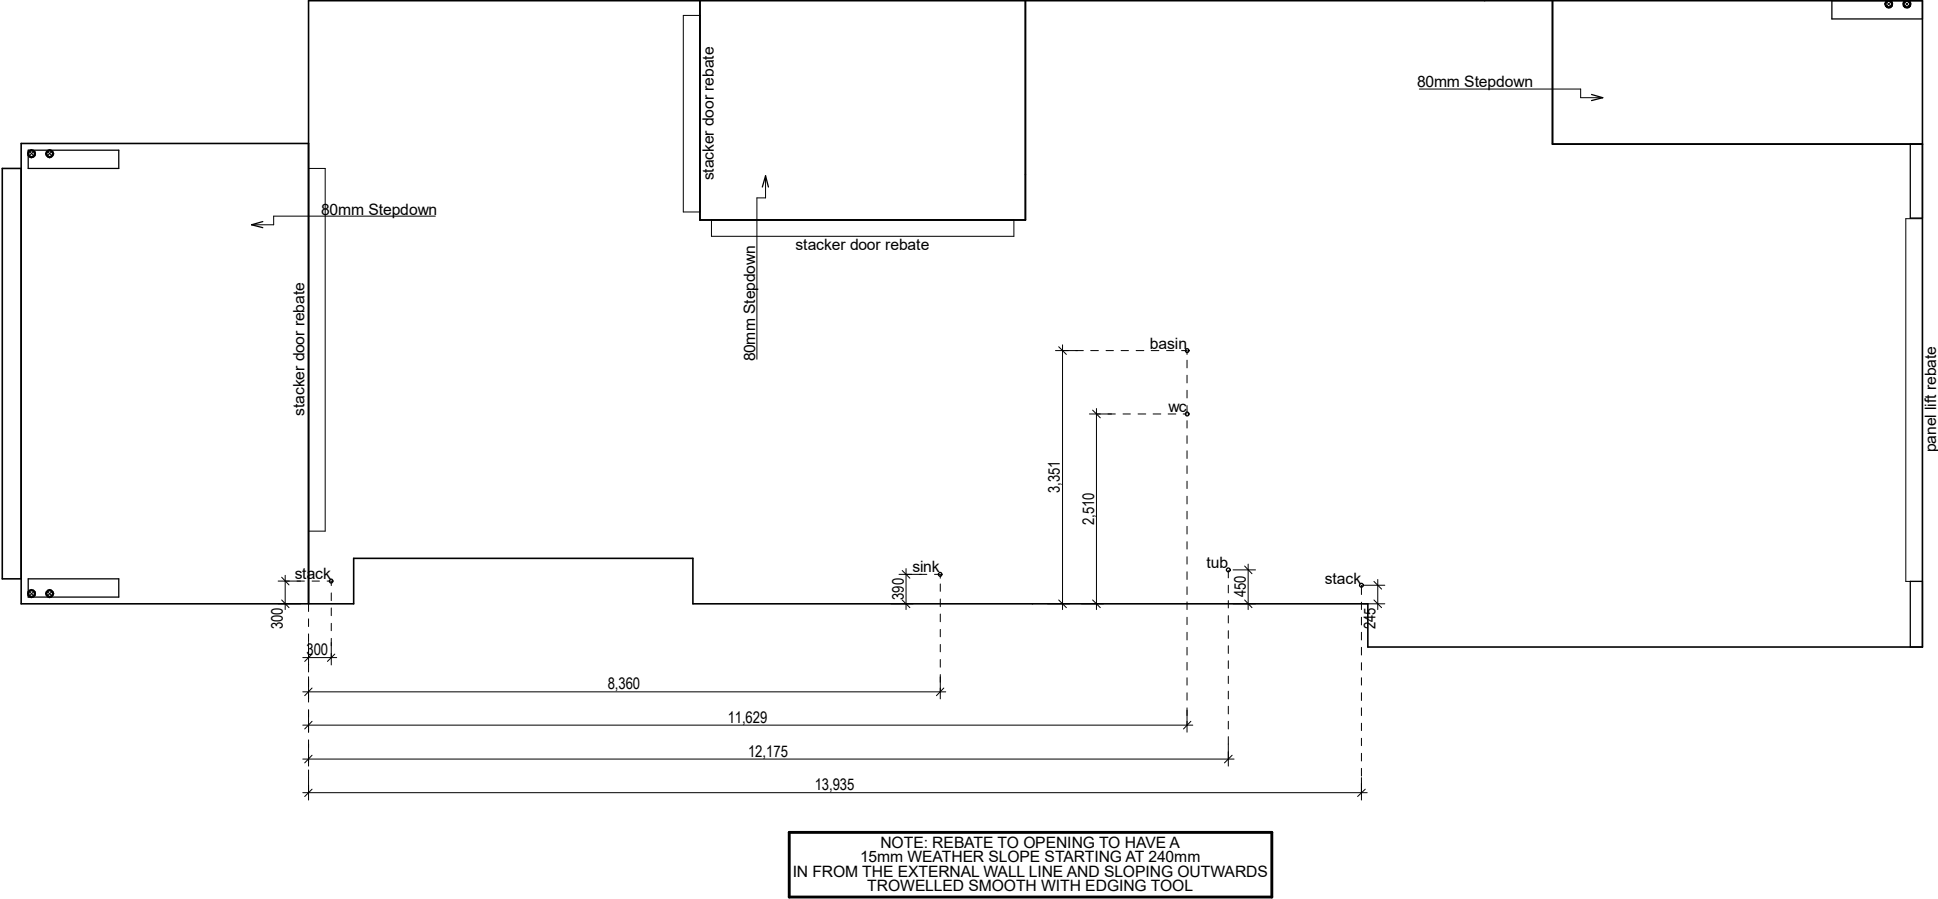

SLAB PENETRATION PLAN

1:100



DRAWING TITLE:

Slab Penetration Plan

DRAWING NO:

10

PROJECT NO:

TMD2221

PROJECT ADDRESS:

32 RICHARDSON STREET
CHELMER QLD 4068

ISSUE DATE:

7TH DECEMBER 2022

REVISION:

Rev M

CLIENT:

L. RICHARDSON


AUTHOR:

TM

DISCLAIMER:


THE PLAN & DESIGN OF THIS HOUSE IS OWNED BY
TMD DESIGN PTY LTD AND UNDER THE
COPYRIGHT ACT OF 1964 CANNOT BE REPRODUCED IN
ANY SHAPE OR FORM WITHOUT PRIOR WRITTEN
CONSENT. ANY DOING SO WILL RESULT IN LIABILITY
UNDER THE ACT.



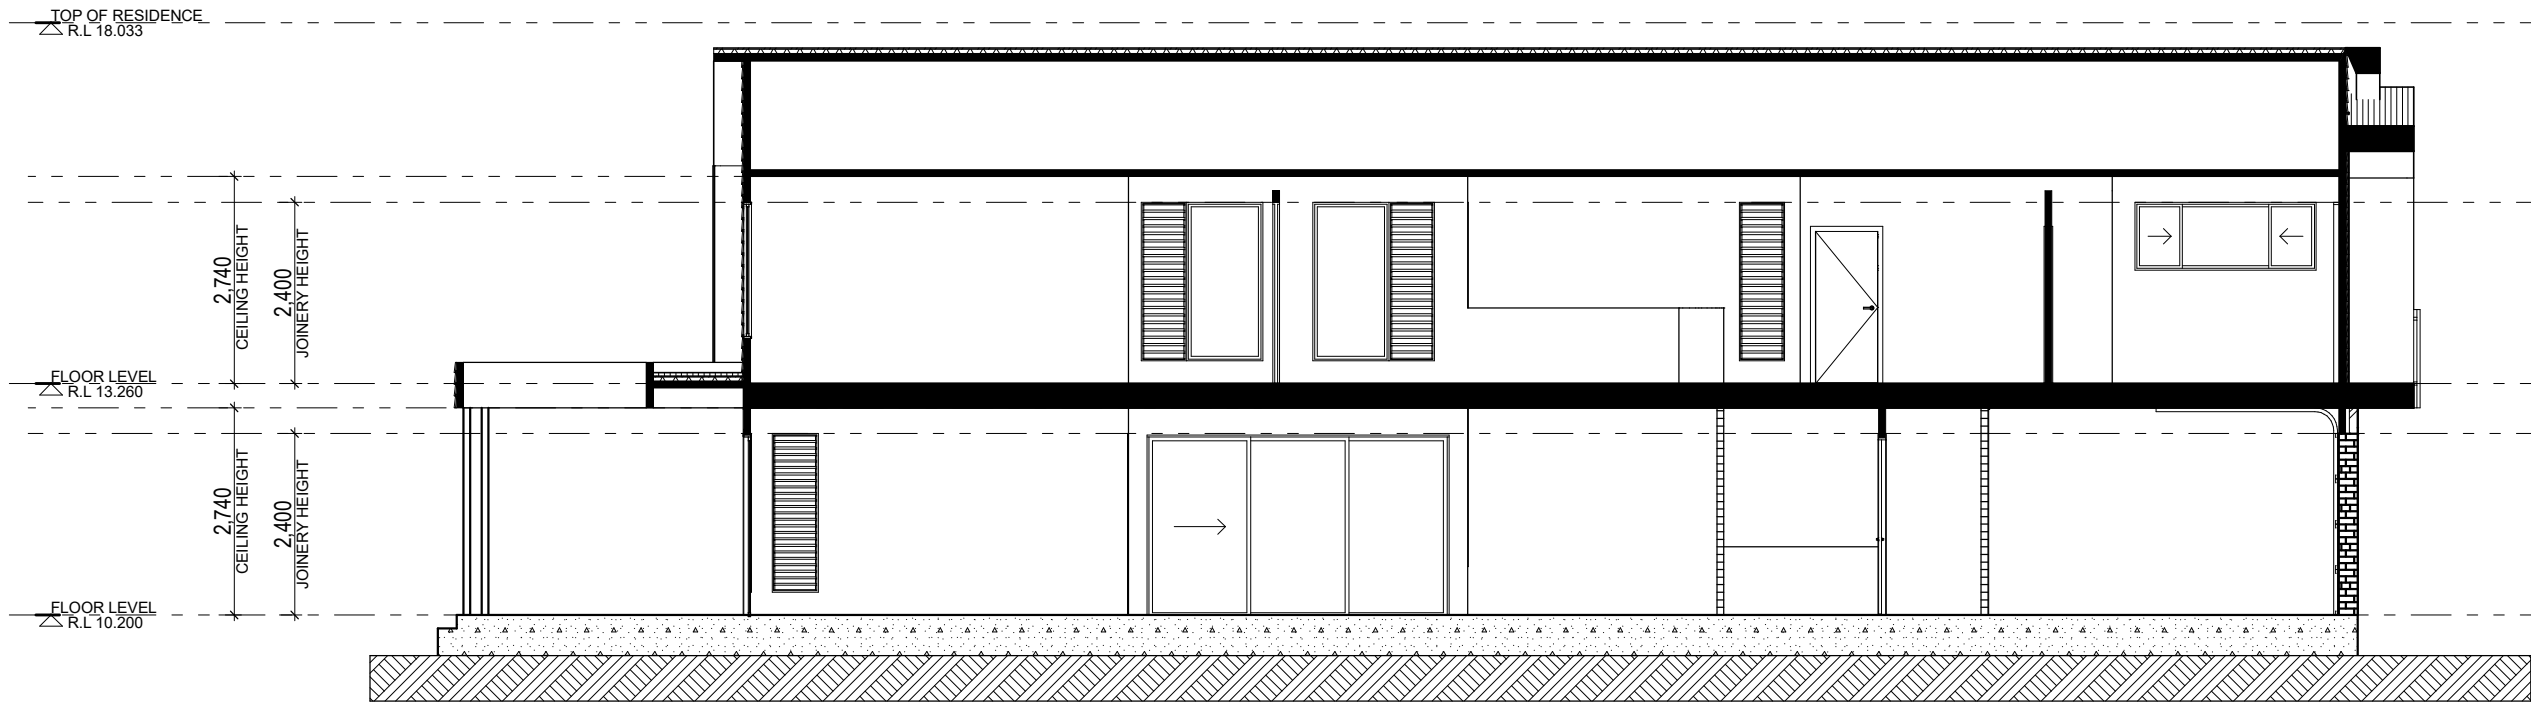

SECTION A-A

1:100

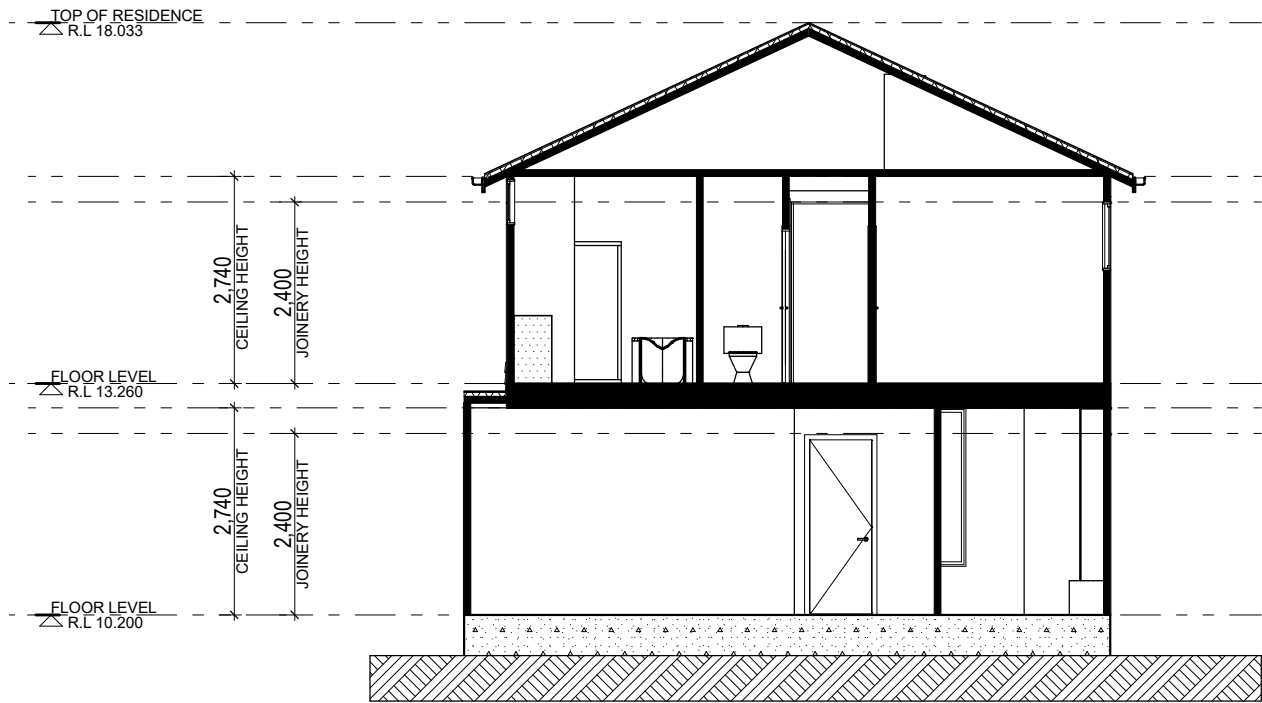

SECTION I-I

1:100

TIMBER SCHEDULE		
GROUND FLOOR		
Load Bearing Wall Studs	70x35 Pine MGP12 @ max. 450c/s	
Noggings	70x35 Pine F5 SEAS	
Top Plate	2/35x70 Pine MGP12	
Bottom Plate	35x70 Pine F5 SEAS	
Non Load Bearing Wall Studs	70x35 Pine F5 SEAS @ max. 600c/s	
Non Load Bearing Top Plates, Bottom Plates, Noggings	70x35 Pine F5 SEAS	
Jamb Studs		
0-1000 Openings	1/70x35 KD Pine MGP12	
1001-1300 Openings	2/70x35 KD Pine MGP12	
1301-1600 Openings	2/70x35 KD Pine MGP12	
1601-1900 Openings	2/70x35 KD Pine MGP12	
1901- 2500 Openings	3/70x35 KD Pine MGP12	
Lintel Sizes		
0-1000 Openings	120 x 35 KD Pine F17 SEAS	
1001-1300 Openings	140 x 35 KD Pine F17 SEAS	
1301-1600 Openings	170 x 35 KD Pine F17 SEAS	
1601-1900 Openings	190 x 35 KD Pine F17 SEAS	
1901- 2500 Openings	2/220 x 35 KD Pine F17 SEAS	

NOTE:
(OTHER TIMBER MEMBERS MAY HAVE BEEN NOTED ON THE PLANS)
(STRUCTURAL ENGINEER TO CERTIFY SELECTED TIMBER MEMBERS. ENGINEERS DETAILS TAKE PRECEDENCE OVER BUILDING DESIGNERS)


(ROOF TRUSS MANUFACTURE TO NOMINATE UPGRADE TO LINTEL SIZES THAT OCCUR UNDER DIRECT ROOF LOADS, i.e GIRDER TRUSSES etc)

(ROOF TRUSS MANUFACTURE TO NOMINATE SPEED BRACING AND FIXINGS)




DRAWING TITLE: Section Views	
DRAWING NO: 11	PROJECT NO: TMD2221
PROJECT ADDRESS: 32 RICHARDSON STREET CHELMER QLD 4068	
ISSUE DATE: 7TH DECEMBER 2022	
REVISION: Rev M	
CLIENT: L. RICHARDSON	
AUTHOR: TM	
DISCLAIMER: THE PLAN & DESIGN OF THIS HOUSE IS OWNED BY MARSHALL DESIGN PTY LTD AND UNDER THE COPYRIGHT ACT OF 1984 CANNOT BE REPRODUCED IN ANY SHAPE OR FORM WITHOUT PRIOR WRITTEN CONSENT. ANY DOING SO WILL RESULT IN LIABILITY UNDER THE ACT.	



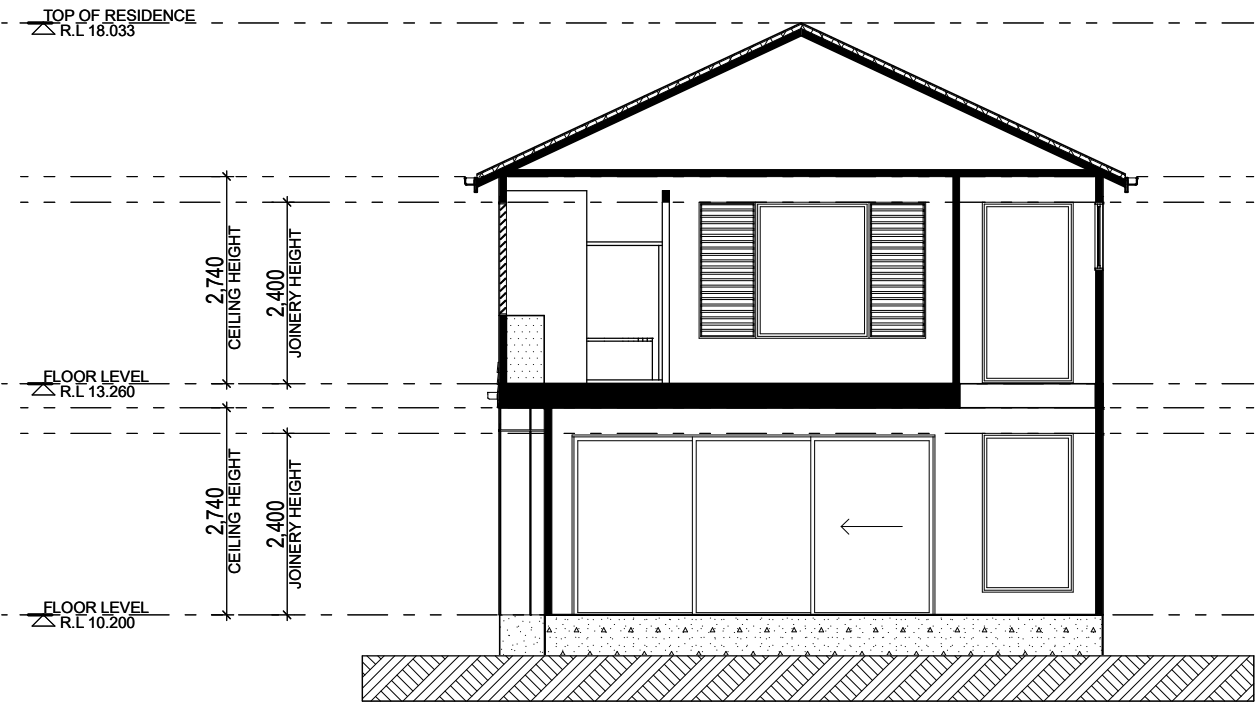

SECTION 2-2 1:100

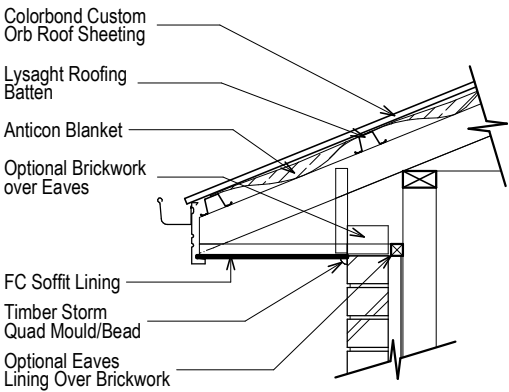

BOXED EAVES DETAIL - BRICK VENEER

TIE-DOWN SCHEDULE	
Roof Sheeting to Battens	Roof Sheet Fixing to manufactures specifications.
Battens to Trusses	Use 1/90mm No.14 Type 17 Screws with 50mm Penetration
Trusses to Top Plates	Use 30 x 0.8mm G.I Loopes Straps & fix with 4/2.8mm dia nails to each end
Top & Bottom Plates to Studs	Use 2/90 x 3.05mm dia. nails with 30 x 0.8 G.I Strap @ every 2nd Stud
Lintels to Studs Alongside Openings	Use 2/30 x 0.8 G.I Strap with 4/2.8mm dia. nails to each end & M10 Bolt to slab
Bottom Plates to Slab	Use One M10 Bolt at not more than 1200mm centres & alongside openings

For Details refer to AS 1684.2 Residential Timber Framed Construction



DRAWING TITLE:

Section Views

DRAWING NO:

12

PROJECT NO:

TMD2221

PROJECT ADDRESS:

32 RICHARDSON STREET
CHELMER QLD 4068

ISSUE DATE:

7TH DECEMBER 2022

REVISION:

Rev M

CLIENT:

L. RICHARDSON

AUTHOR:



TM

DISCLAIMER:

THE PLAN & DESIGN OF THIS HOUSE IS OWNED BY
TMRSHALL DESIGN PTY LTD AND UNDER THE
COPYRIGHT ACT OF 1984 CANNOT BE REPRODUCED IN
ANY SHAPE OR FORM WITHOUT PRIOR WRITTEN
CONSENT. ANY DOING SO WILL RESULT IN LIABILITY
UNDER THE ACT.



CTRICAL LEGEND		QTY.
	SINGLE GPO	6
	DOUBLE GPO	35
	WEATHER PROOF GPO	2
	TELEVISION POINT	2
	PHONE POINT	1
	DATA POINT	2
	FOXTEL POINT	0
	LED DOWNLIGHT	60
	PENDANT (OWNER SUP.)	0
	STAIRLIGHT (OWNER SUP.)	0
	STRIP FLUORO LIGHT	2
	EXHAUST FAN	2
	IXL	2
	DOWN DIRECTIONAL	2
	BUNKER	3
	SMOKE ALARM	
	CEILING FAN (WHITE)	4
	CEILING FAN WITH LIGHT	0
USIONS		
IGLE PHASE ELECTRICITY SUPPLY		
ECTRIC HOT WATER CIRCUIT		
T PLATE CIRCUIT		
EN CIRCUIT		
NGE HOOD POWER SUPPLY		
DERGROUND MAINS SUPPLY		
USE EARTHING		
2-WAY SWITCHES (STAIRS,HALLWAY + MASTER)		

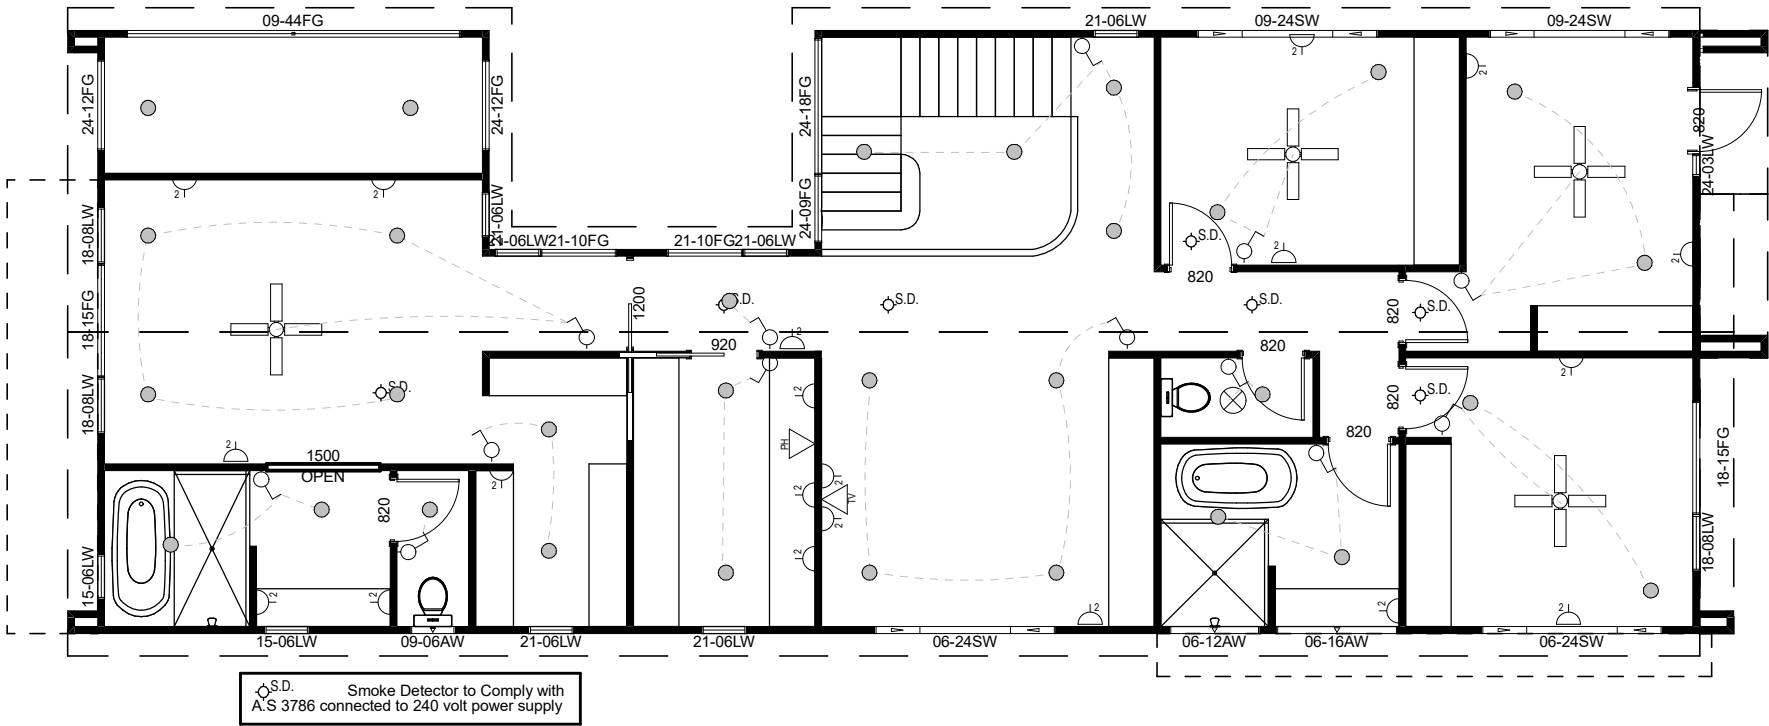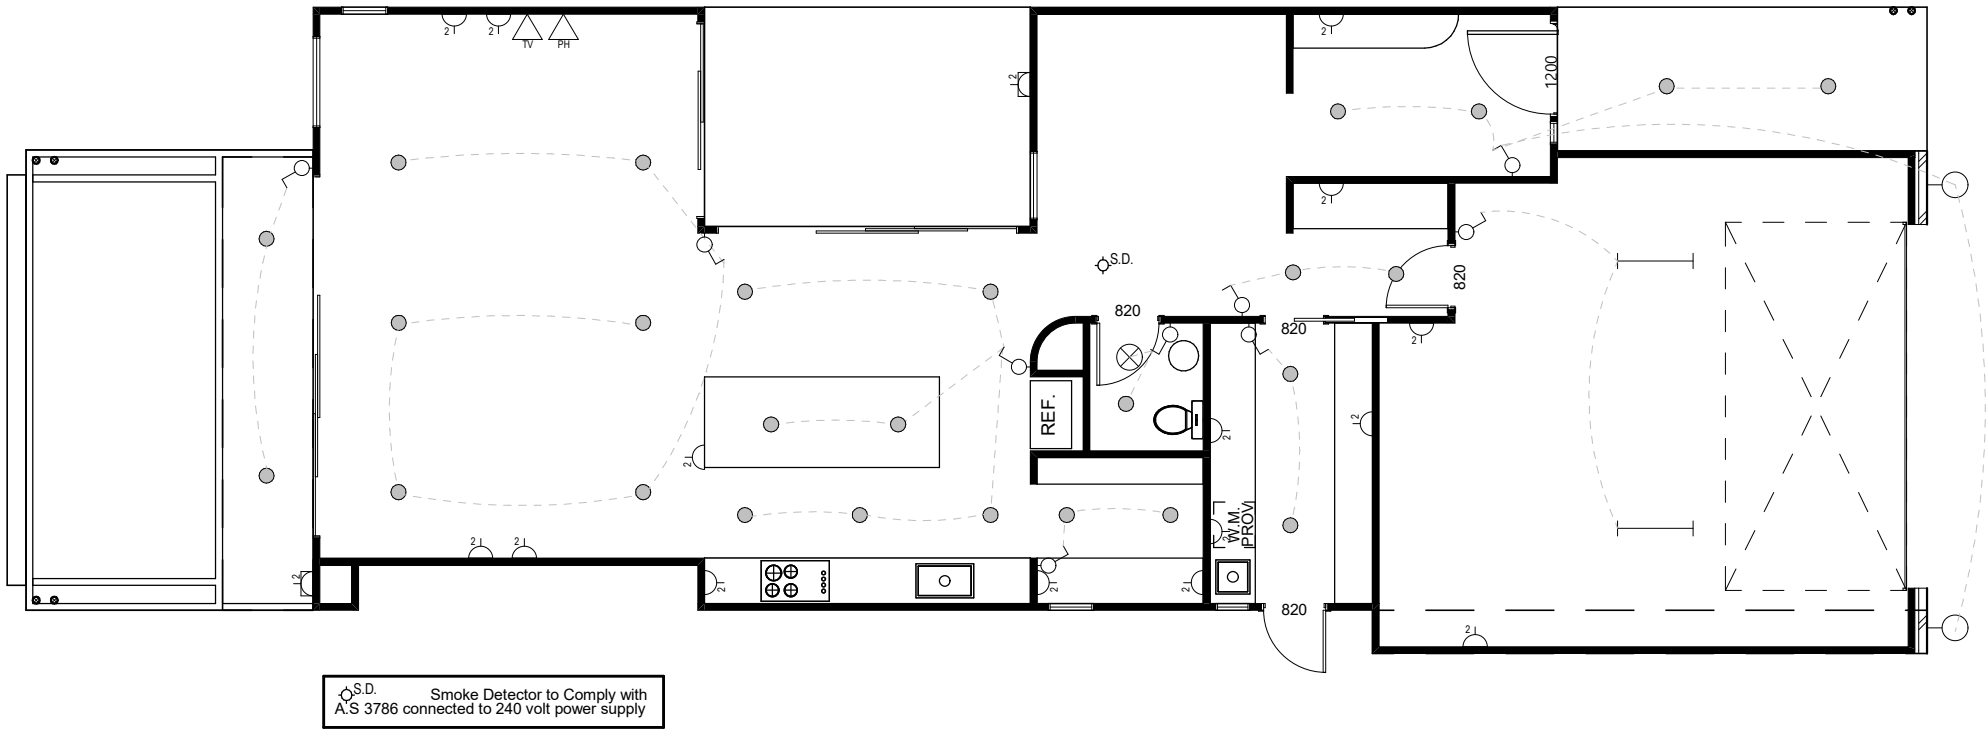

tmd.

DRAWING TITLE:
Electrical Plan

DRAWING NO:
13

PROJECT NO:
TMD2221

PROJECT ADDRESS:
**32 RICHARDSON STREET
CHELMER QLD 4068**

ISSUE DATE:
7TH DECEMBER 2022

REVISION:
Rev M

CLIENT:
L. RICHARDSON

AUTHOR:
TM

DISCLAIMER:
THE PLAN & DESIGN OF THIS HOUSE IS OWNED BY
TMARSHALL DESIGN PTY LTD AND UNDER THE
COPYRIGHT ACT OF 1984 CANNOT BE REPRODUCED IN
ANY SHAPE OR FORM WITHOUT PRIOR WRITTEN
CONSENT. ANY DOING SO WILL RESULT IN LIABILITY
UNDER THE ACT.

©

BRACING SCHEDULE

ALL BRACING DESIGNED TO: N2

GROUND FLOOR:

DIRECTION A:



Brace Type:

A1 - PLYWOOD (to compy with AS 1684.2 1999 and Table 8.18(h))

No. of Panels: 23.40m @ 6.0Kn/m
Total: 140.40 Kn

TOTAL Kn REQUIRED = 138.00 Kn
TOTAL Kn ACHIEVED = 140.40 Kn

DIRECTION B:




Brace Type:

B1 - PLYWOOD (to compy with AS 1684.2 1999 and Table 8.18(h))


No. of Panels: 10.80m @ 6.0Kn/m
Total: 64.80 Kn

TOTAL Kn REQUIRED = 41.62 Kn
TOTAL Kn ACHIEVED = 64.80 Kn

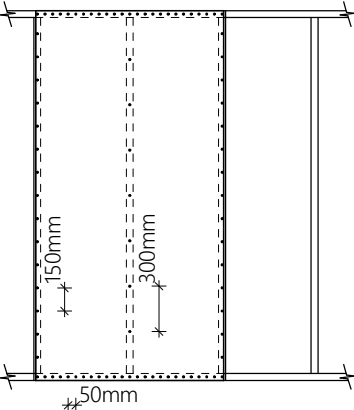

A1 & B1 - PLYWOOD SHEET
(to compy with AS 1684.2 1999 and Table 8.18(h)) Method B

BRACING LEGEND:
900mm WIDE PLYWOOD SHEETS SHALL BE NAILED TO FRAME USING 30 x 2.8dia. GALVANISED FLATHEAD NAILS OR EQUIVALANT.
PLYWOOD STRESS GRADE F8-9mm THICK, F11-7mm THICK, F14-6mm THICK AND F27-4.5

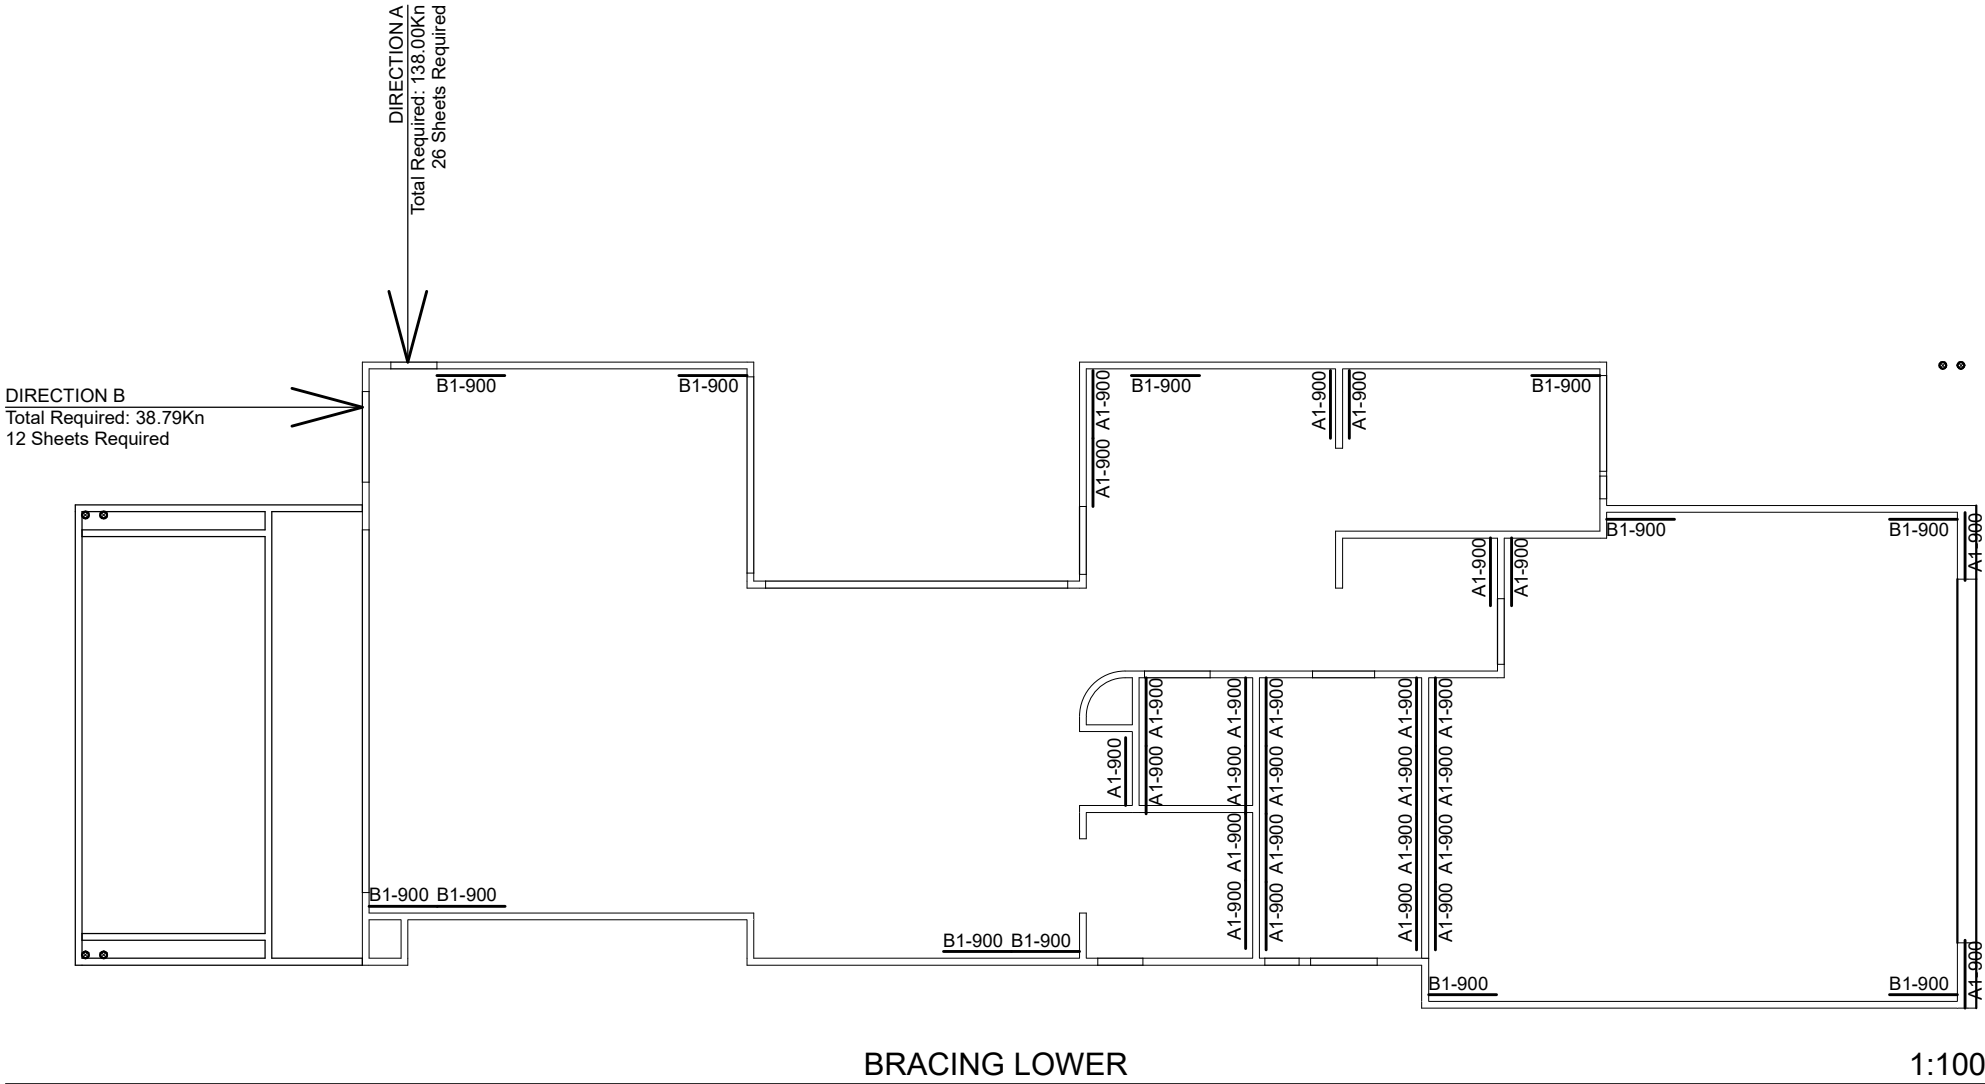

DRAWING TITLE:

Ground Bracing

DRAWING NO:

14

PROJECT NO:

TMD2221

PROJECT ADDRESS:

32 RICHARDSON STREET
CHELMER QLD 4068

ISSUE DATE:

7TH DECEMBER 2022

REVISION:

Rev M

CLIENT:

L. RICHARDSON

AUTHOR:

TM

DISCLAIMER:

THE PLAN & DESIGN OF THIS HOUSE IS OWNED BY TMARSHALL DESIGN PTY LTD AND UNDER THE COPYRIGHT ACT OF 1964 CANNOT BE REPRODUCED IN ANY SHAPE OR FORM WITHOUT PRIOR WRITTEN CONSENT. ANY DOING SO WILL RESULT IN LIABILITY UNDER THE ACT.



BRACING SCHEDULE

ALL BRACING DESIGNED TO: N2

FIRST FLOOR:

DIRECTION A:

Brace Type:
A1 - PLYWOOD (to compy with
AS 1684.2 1999 and Table 8.18(h))

No. of Panels: Total:
13.50m @ 6.0Kn/m 81.00 Kn


TOTAL Kn REQUIRED = 70.09 Kn
TOTAL Kn ACHIEVED = 81.00 Kn

DIRECTION B:

Brace Type:
B1 - PLYWOOD (to compy with
AS 1684.2 1999 and Table 8.18(h))

No. of Panels: Total:
8.10m @ 6.0Kn/m 48.60 Kn


TOTAL Kn REQUIRED = 19.32 Kn
TOTAL Kn ACHIEVED = 48.60 Kn

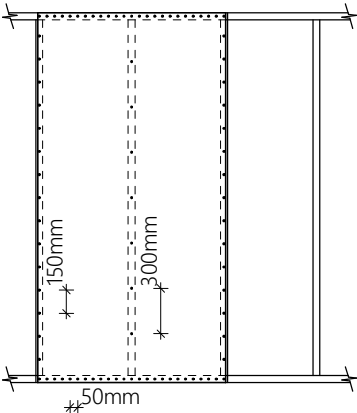

A1 & B1 - PLYWOOD SHEET
(to compy with AS 1684.2 1999
and Table 8.18(h)) Method B

BRACING LEGEND:

900mm WIDE PLYWOOD SHEETS
SHALL BE NAILED TO FRAME
USING 30 x 2.8dia. GALVANISED
FLATHEAD NAILS OR
EQUIVALANT.
PLYWOOD STRESS GRADE F8-
9mm
THICK, F11-7mm THICK, F14-6mm
THICK AND F27-4.5

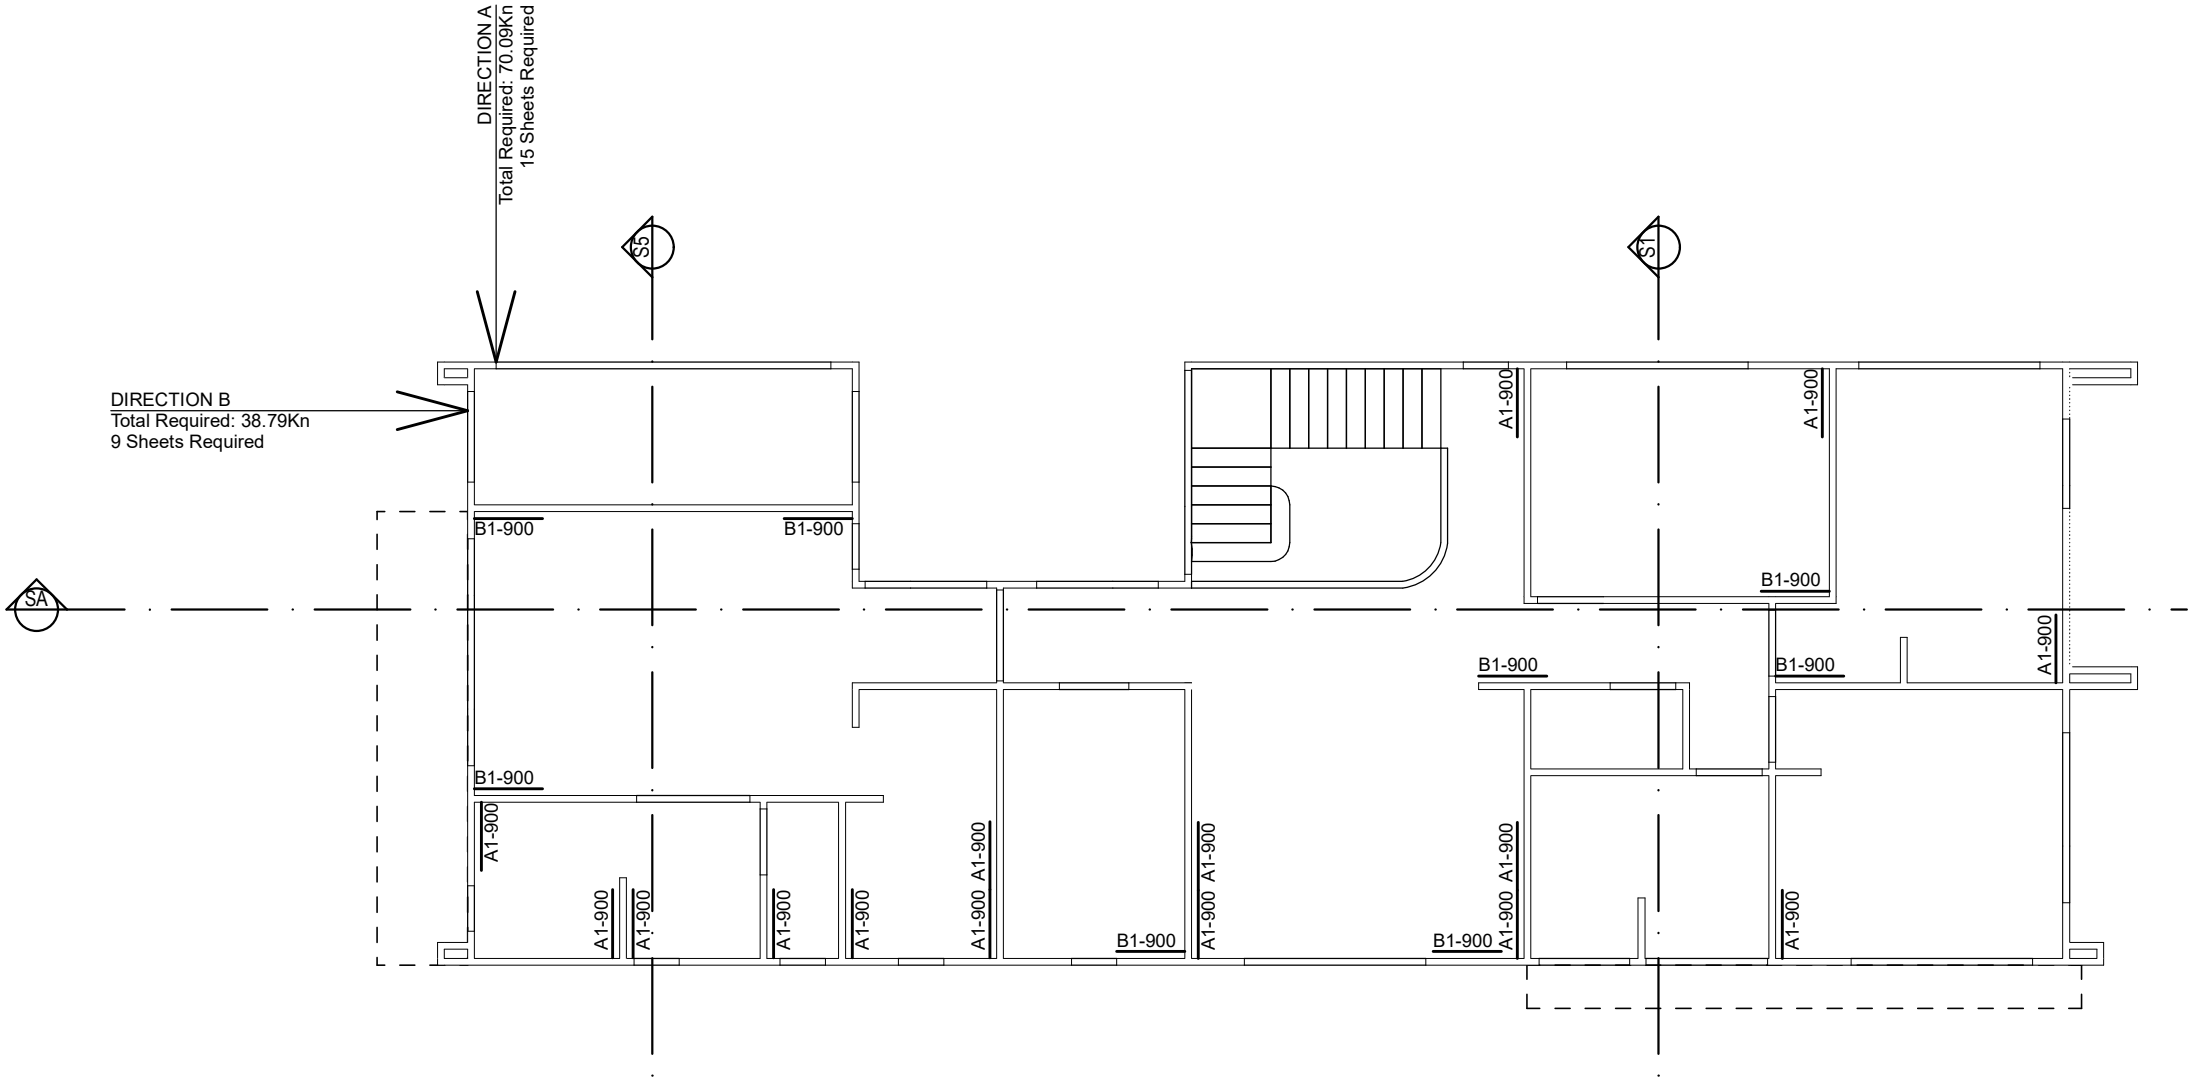

BRACING UPPER

1:100



DRAWING TITLE:

Upper Bracing

DRAWING NO:

15

PROJECT NO:

TMD2221

PROJECT ADDRESS:

32 RICHARDSON STREET
CHELMER QLD 4068

ISSUE DATE:

7TH DECEMBER 2022

REVISION:

Rev M

CLIENT:

L. RICHARDSON


AUTHOR:

TM


DISCLAIMER:

THE PLAN & DESIGN OF THIS HOUSE IS OWNED BY
MARSHALL DESIGN PTY LTD AND UNDER THE
COPYRIGHT ACT OF 1984 CANNOT BE REPRODUCED IN
ANY SHAPE OR FORM WITHOUT PRIOR WRITTEN
CONSENT. ANY DOING SO WILL RESULT IN LIABILITY
UNDER THE ACT.




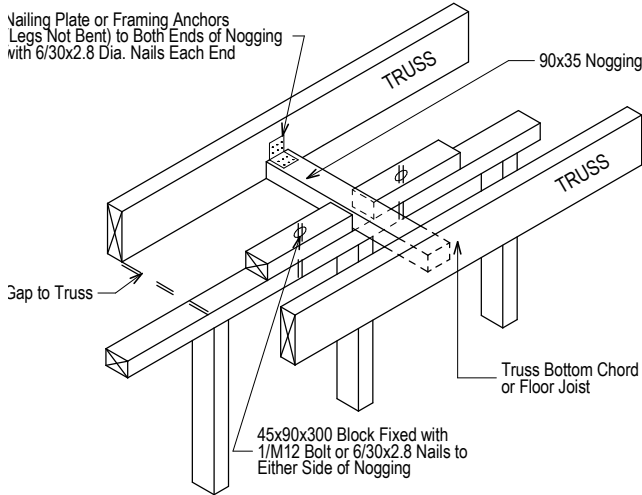


PARALLEL TO TRUSS
PROVIDE TWO CONNECTIONS FOR EVERY 1.2m LENGTH OF BRACING WALL

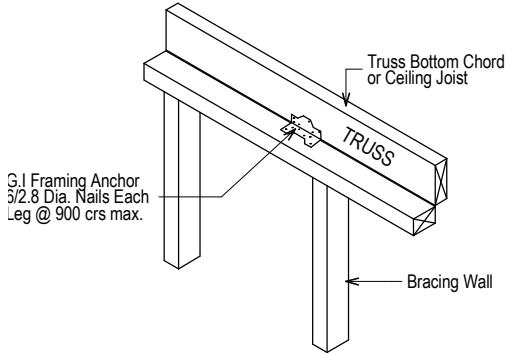


PARALLEL TP TRUSSES OR CEILING JOISTS
PROVIDE TWO CONNECTIONS FOR EVERY 1.2m LENGTH OF BRACING WALL

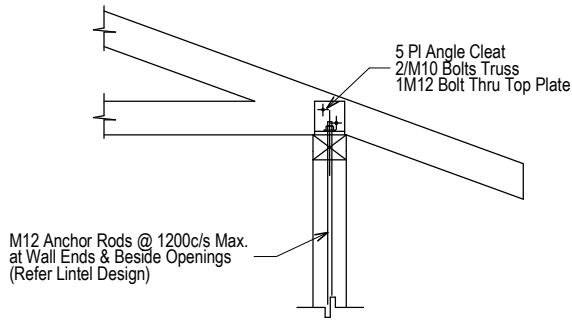


TRUSS HOLD DOWN DETAIL

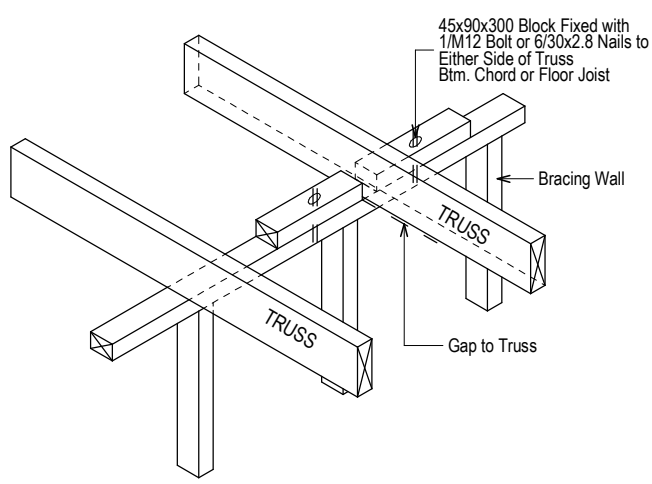


PERPENDICULAR TO TRUSS

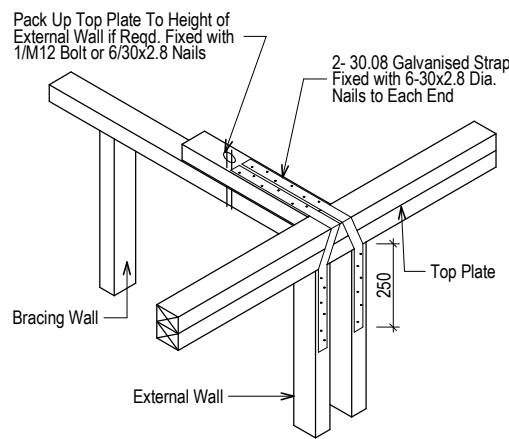


PERPENDICULAR TO WALL
PROVIDE TWO CONNECTIONS FOR EVERY 1.2m LENGTH OF BRACING WALL

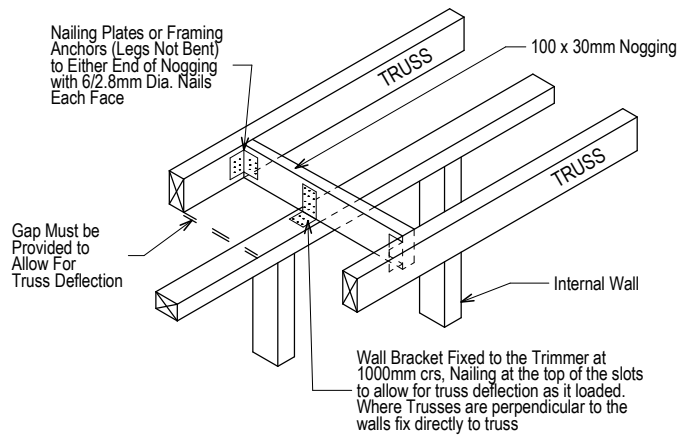


NON LOAD BEARING WALL PARALLEL TO TRUSSES

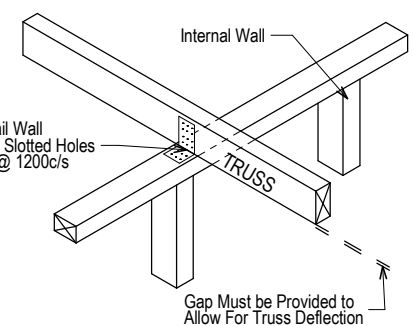


NON LOADBEARING WALL
PERPENDICULAR TO TRUSSES

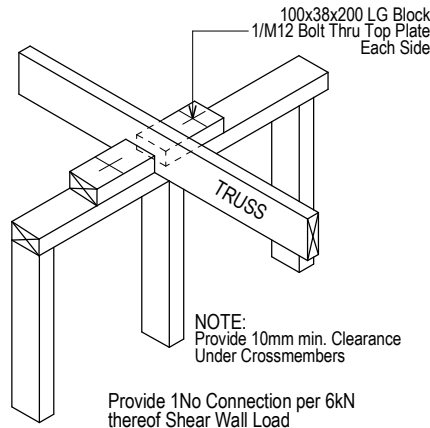

TRUSS CONNECTION TO INTERNAL SHEAR WALL
TRUSSES NORMAL TO WALL

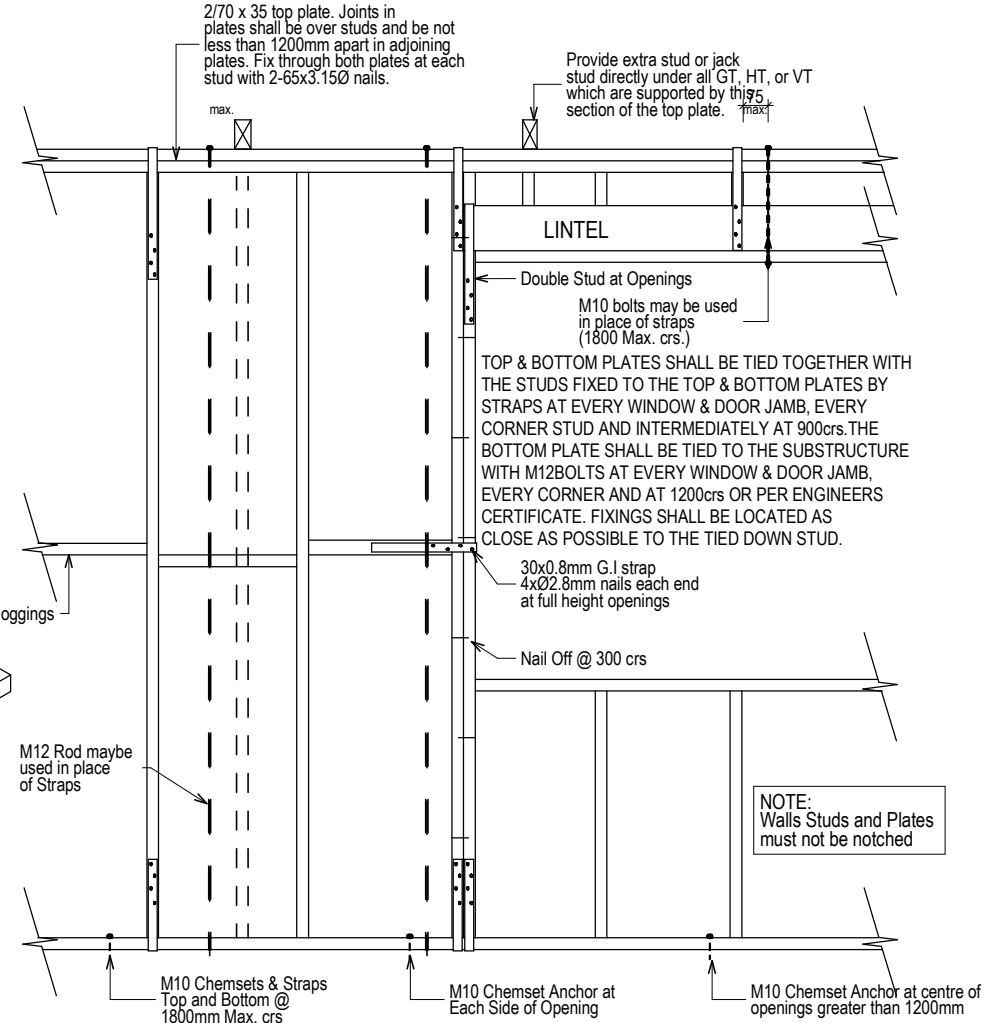

TYPICAL TIEDOWN DETAIL

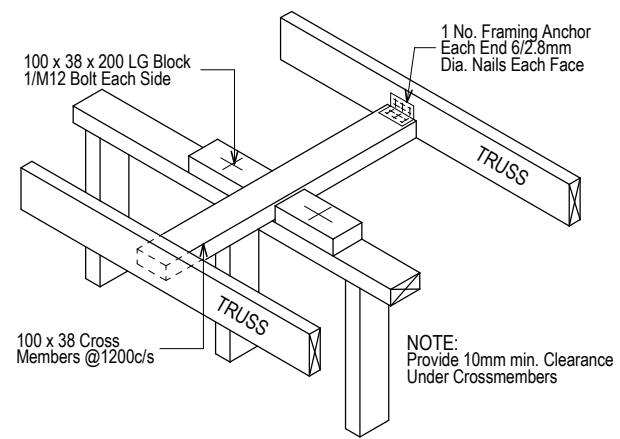

TRUSS CONNECTION TO INTERNAL SHEAR WALL
TRUSSES PARALLEL TO WALL



DRAWING TITLE: Tie Down Details	
DRAWING NO: 16	PROJECT NO: TMD2221
PROJECT ADDRESS: 32 RICHARDSON STREET CHELMER QLD 4068	
ISSUE DATE: 7TH DECEMBER 2022	
REVISION: Rev M	
CLIENT: L. RICHARDSON	
AUTHOR: TM	

DISCLAIMER:
THE PLAN & DESIGN OF THIS HOUSE IS OWNED BY THARSHALL DESIGN PTY LTD AND UNDER THE COPYRIGHT ACT OF 1964 CANNOT BE REPRODUCED IN ANY SHAPE OR FORM WITHOUT PRIOR WRITTEN CONSENT. ANY DOING SO WILL RESULT IN LIABILITY UNDER THE ACT.

